



Дизайн-проект медицинского центра 2025г

ПО АДРЕСУ: г. Кемерово, ул. Николая Островского, 27


Выполнил дизайнер Ксения Кукушкина

8-913-307-23-75


Содержание

План левого крыла медицинского центра после перепланировки	1
План левого крыла медицинского центра с расстановкой мебели	2
План потолков левого крыла медицинского центра	3
План левого крыла медицинского центра с размещением осветительных приборов	4
План левого крыла медицинского центра с привязками выключателей и указанием включения групп светильников	5
План маркировок левого крыла медицинского центра	6
План правого крыла медицинского центра после перепланировки	7
План правого крыла медицинского центра с расстановкой мебели	8
План потолков правого крыла медицинского центра	9
План правого крыла медицинского центра с размещением осветительных приборов	10
План правого крыла медицинского центра с привязками выключателей и указанием включения групп светильников	11
План маркировок правого крыла медицинского центра	12
Развертки зоны входа	13
Развертки зоны регистратуры	14
Развертки зоны коридора №1	15
Развертки зоны коридора №2	16
3Д картинки левого крыла медицинского центра	17-22


План левого крыла медицинского центра после перепланировки

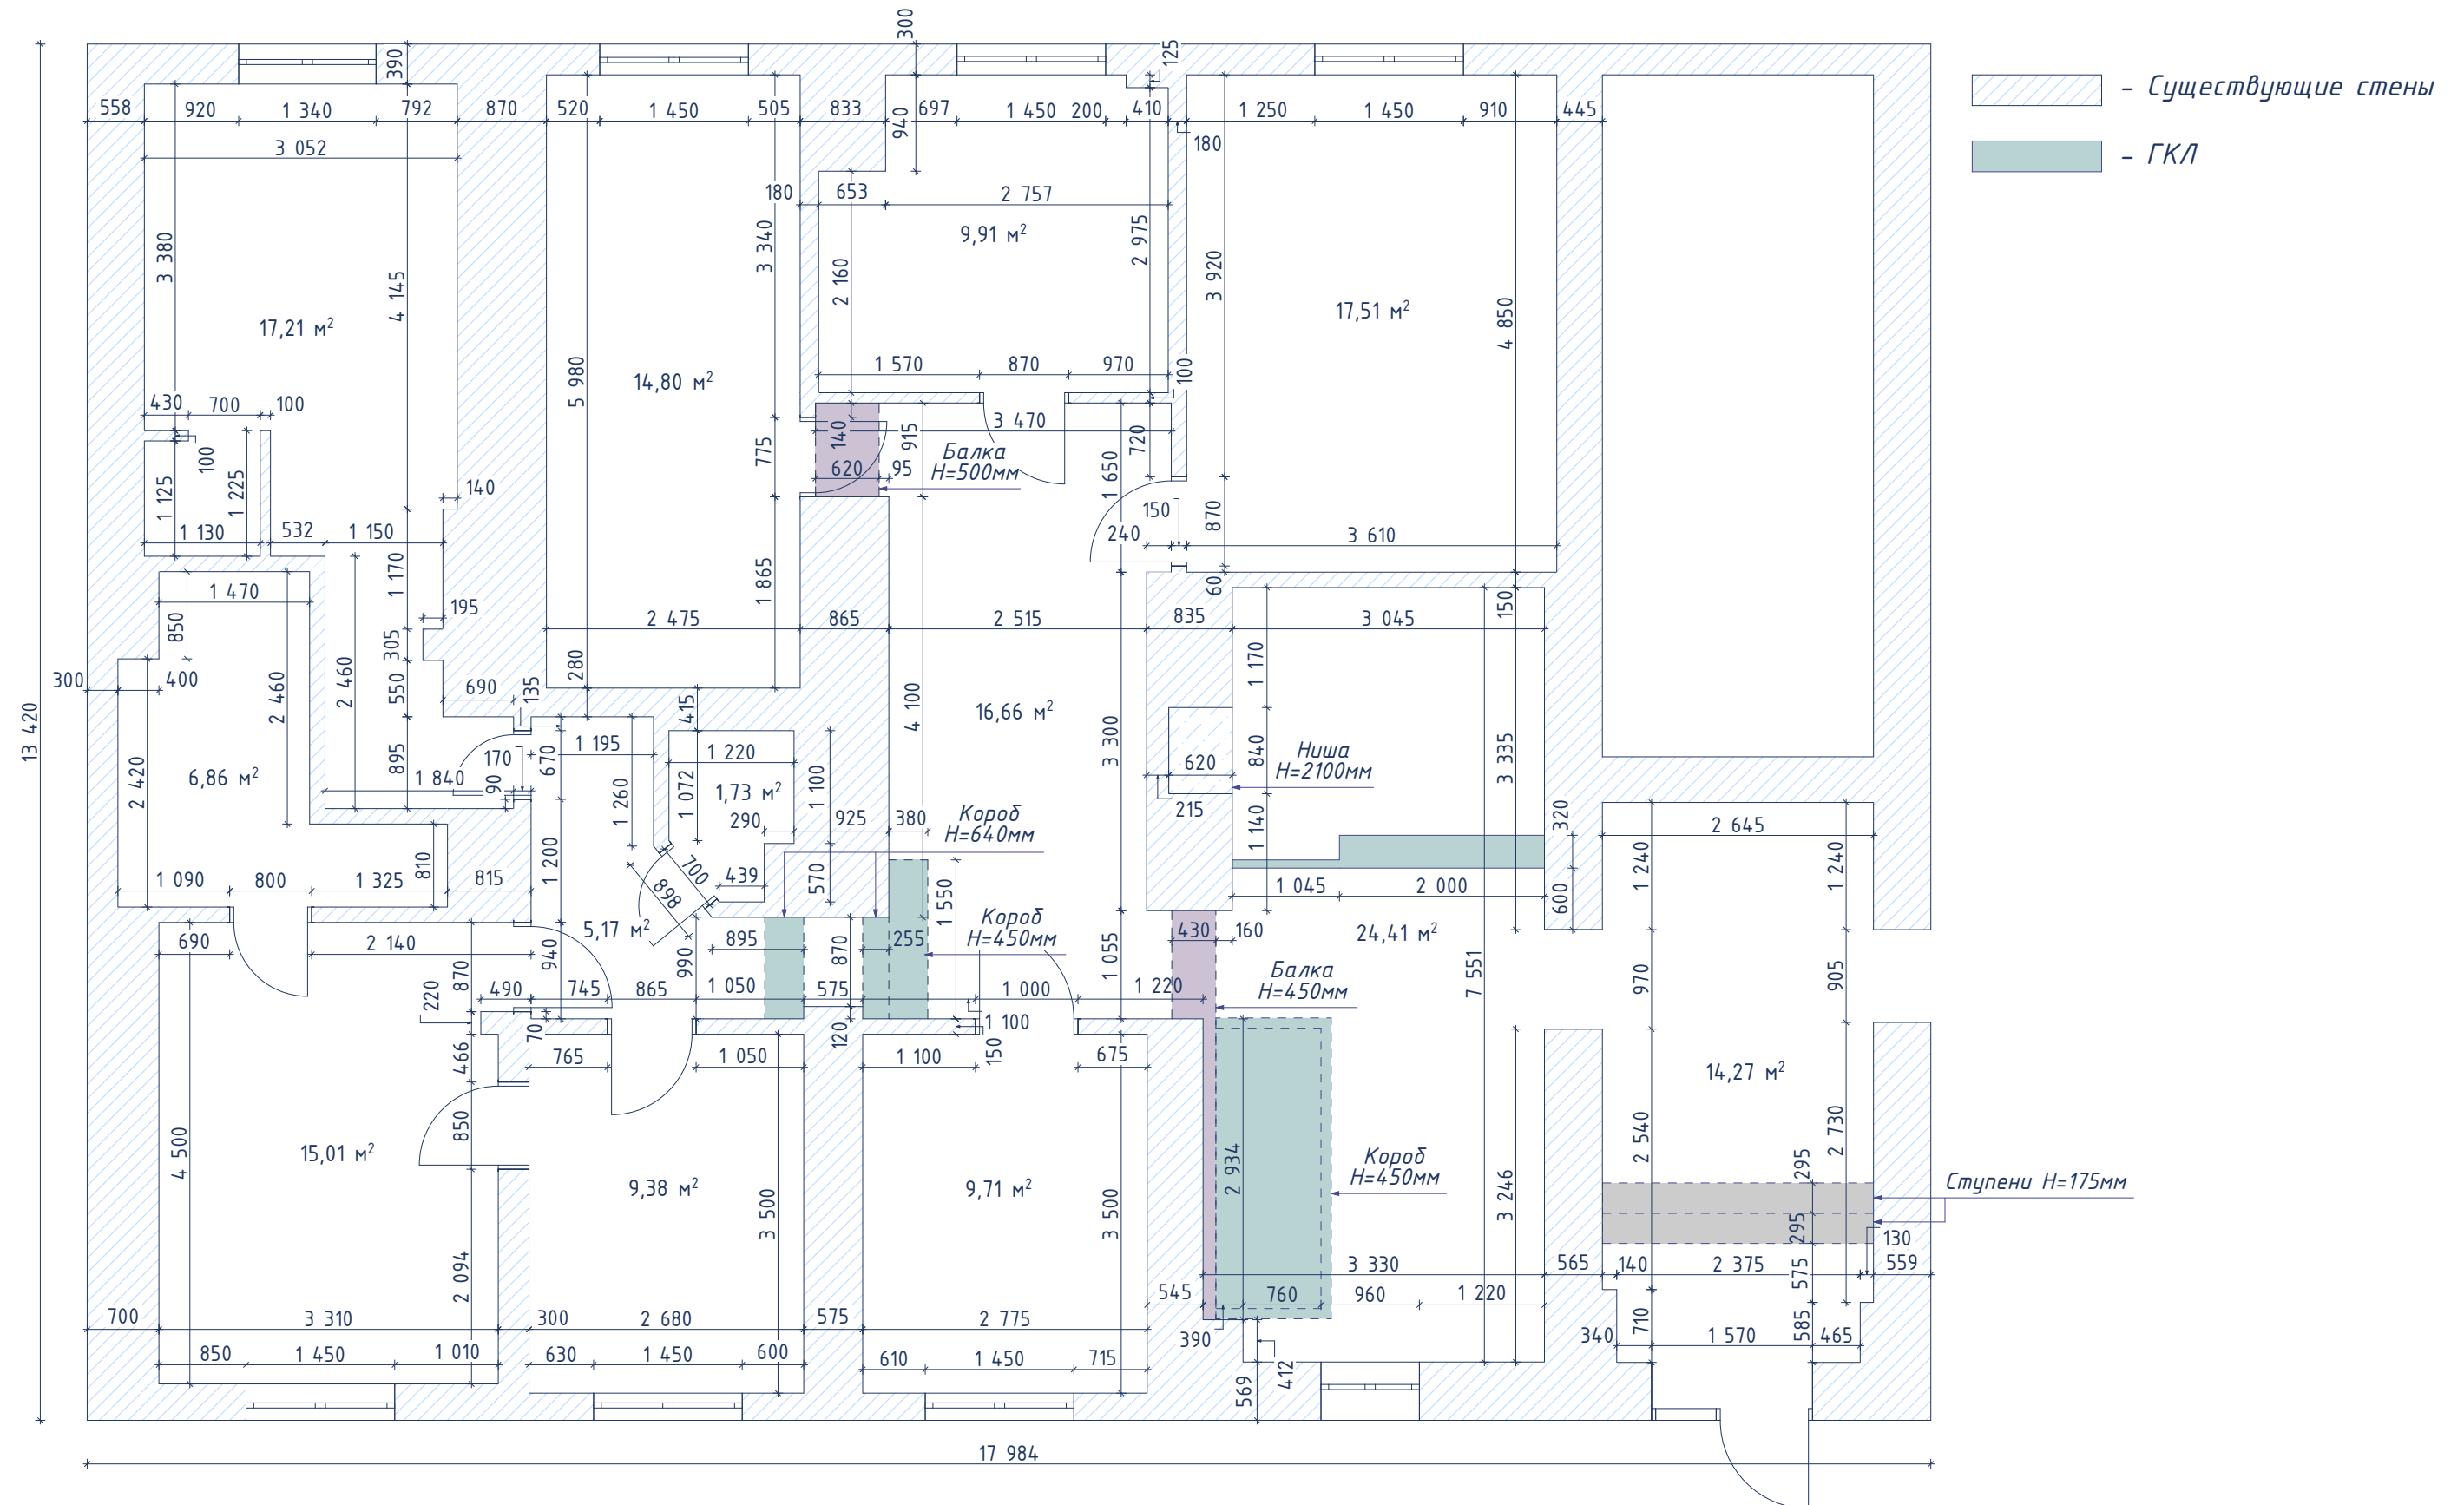


План расстановки мебели левого крыла медицинского центра

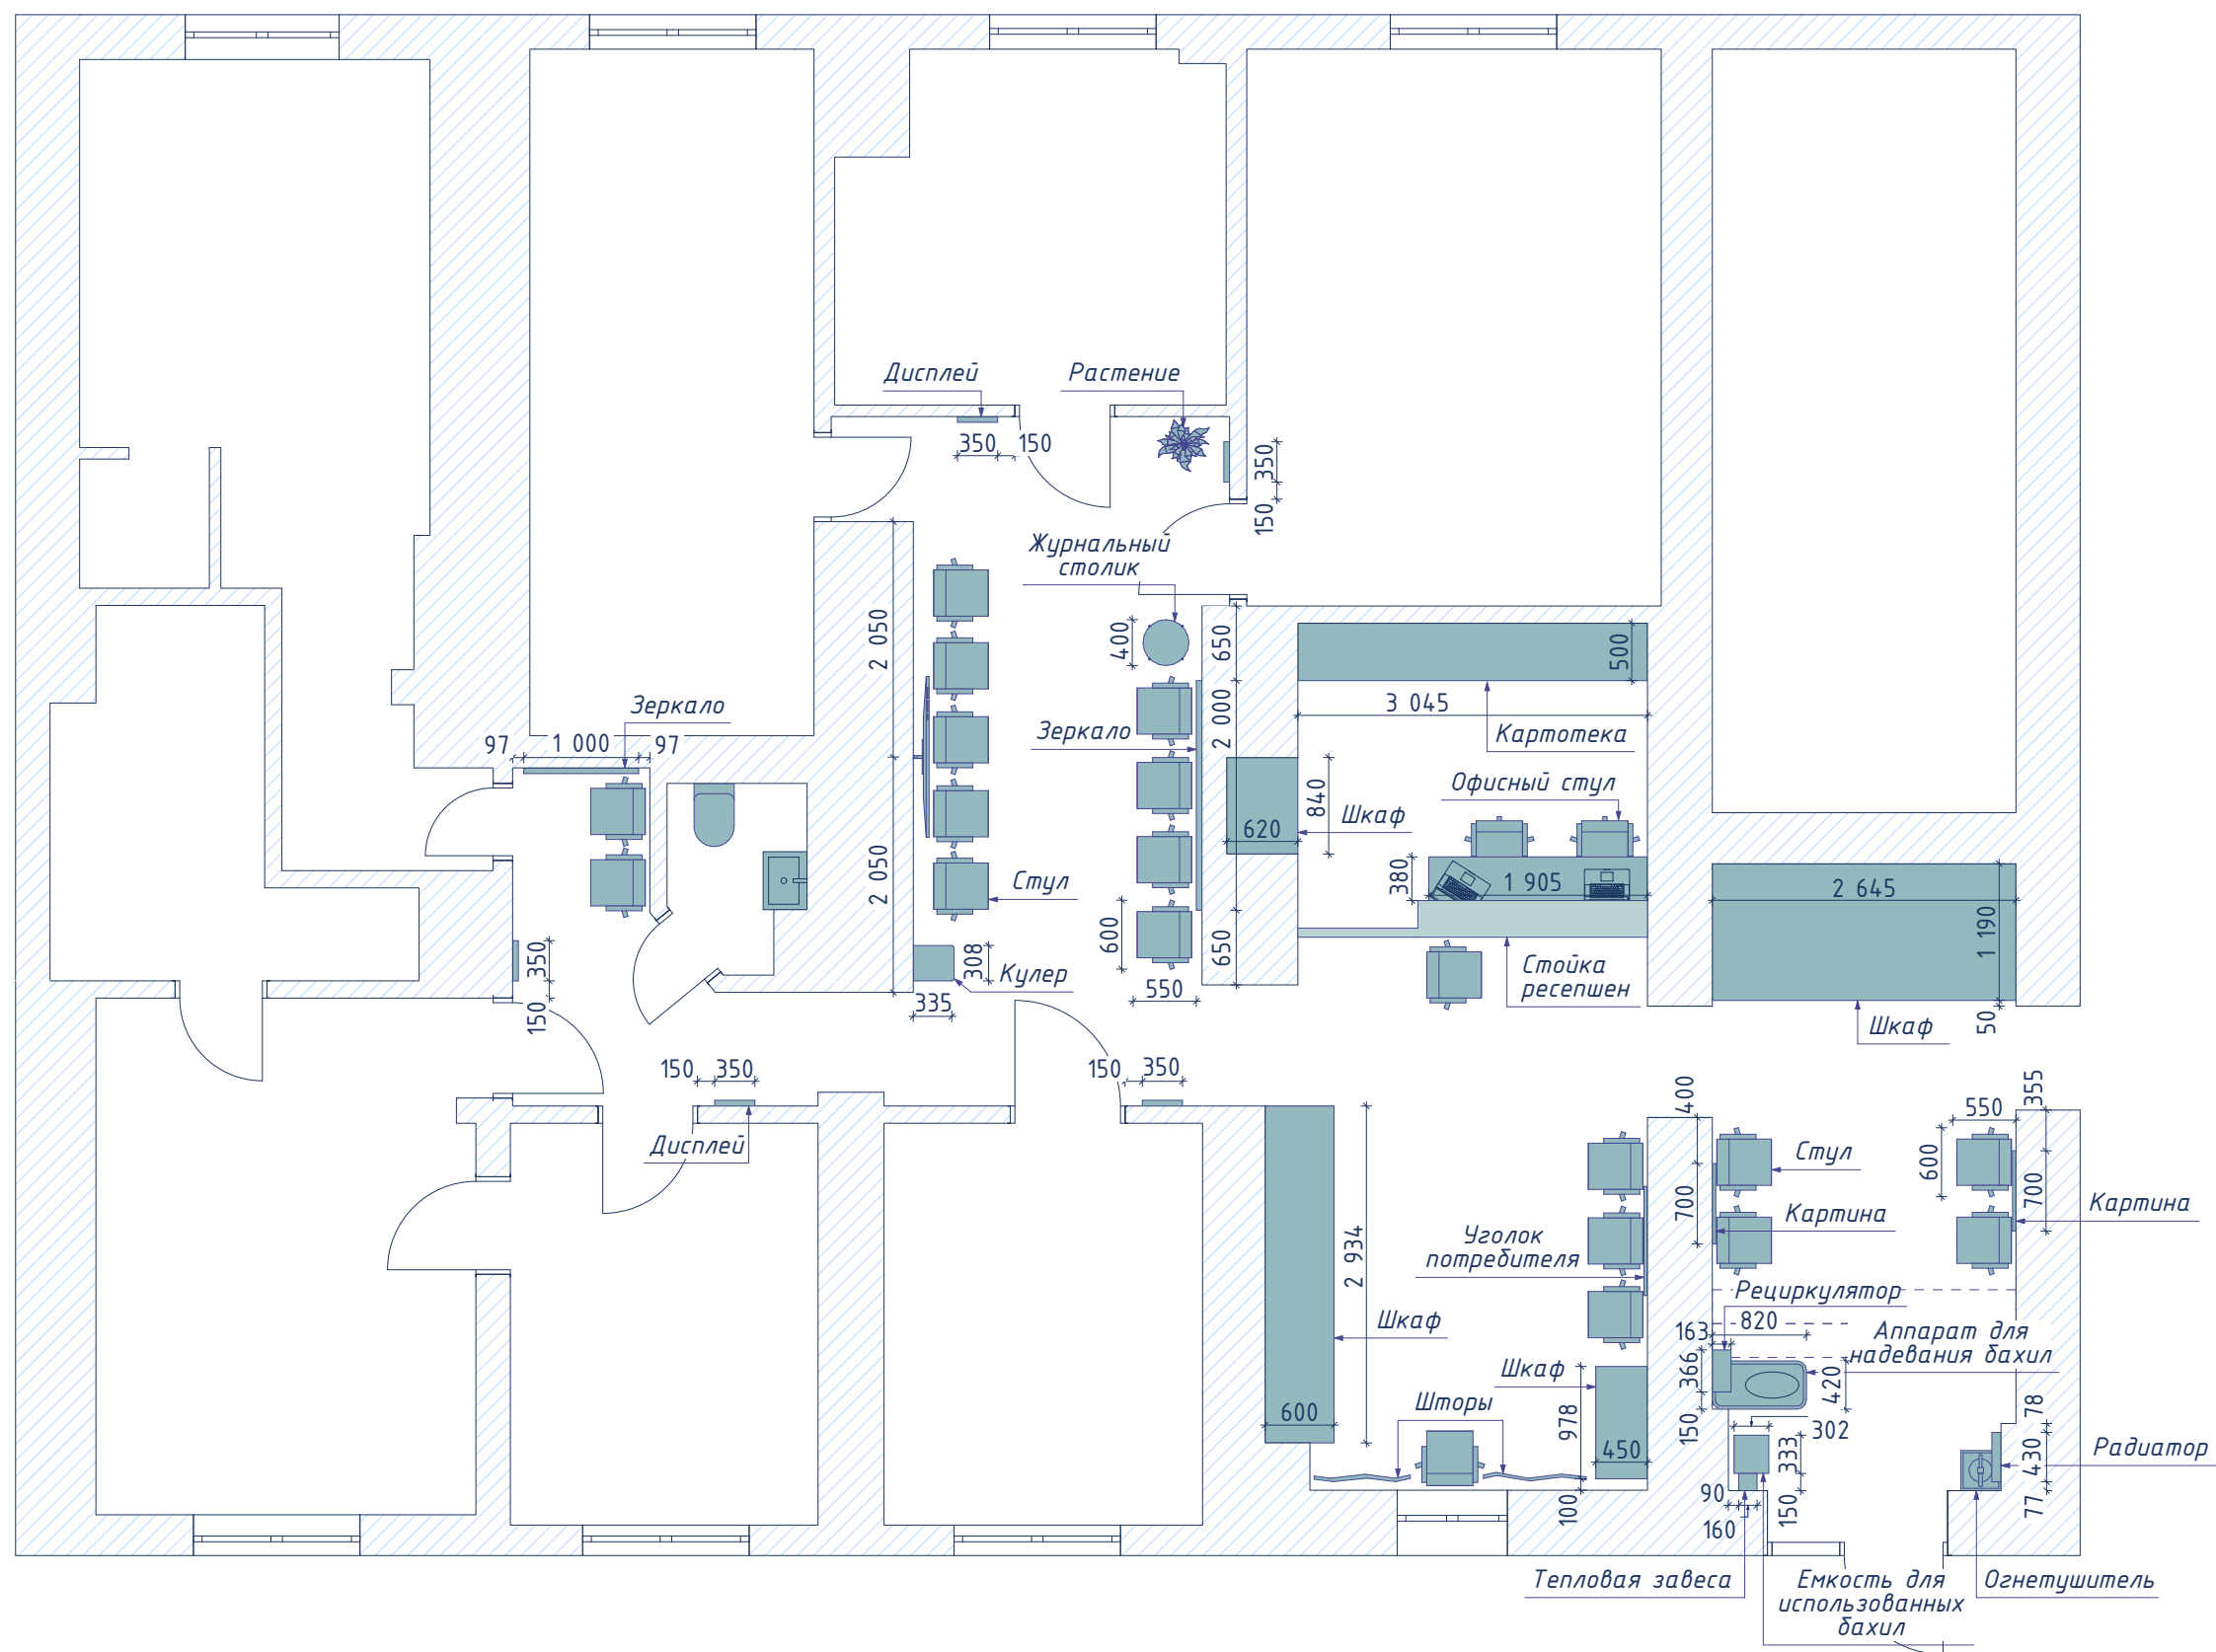


План потолков левого крыла медицинского центра

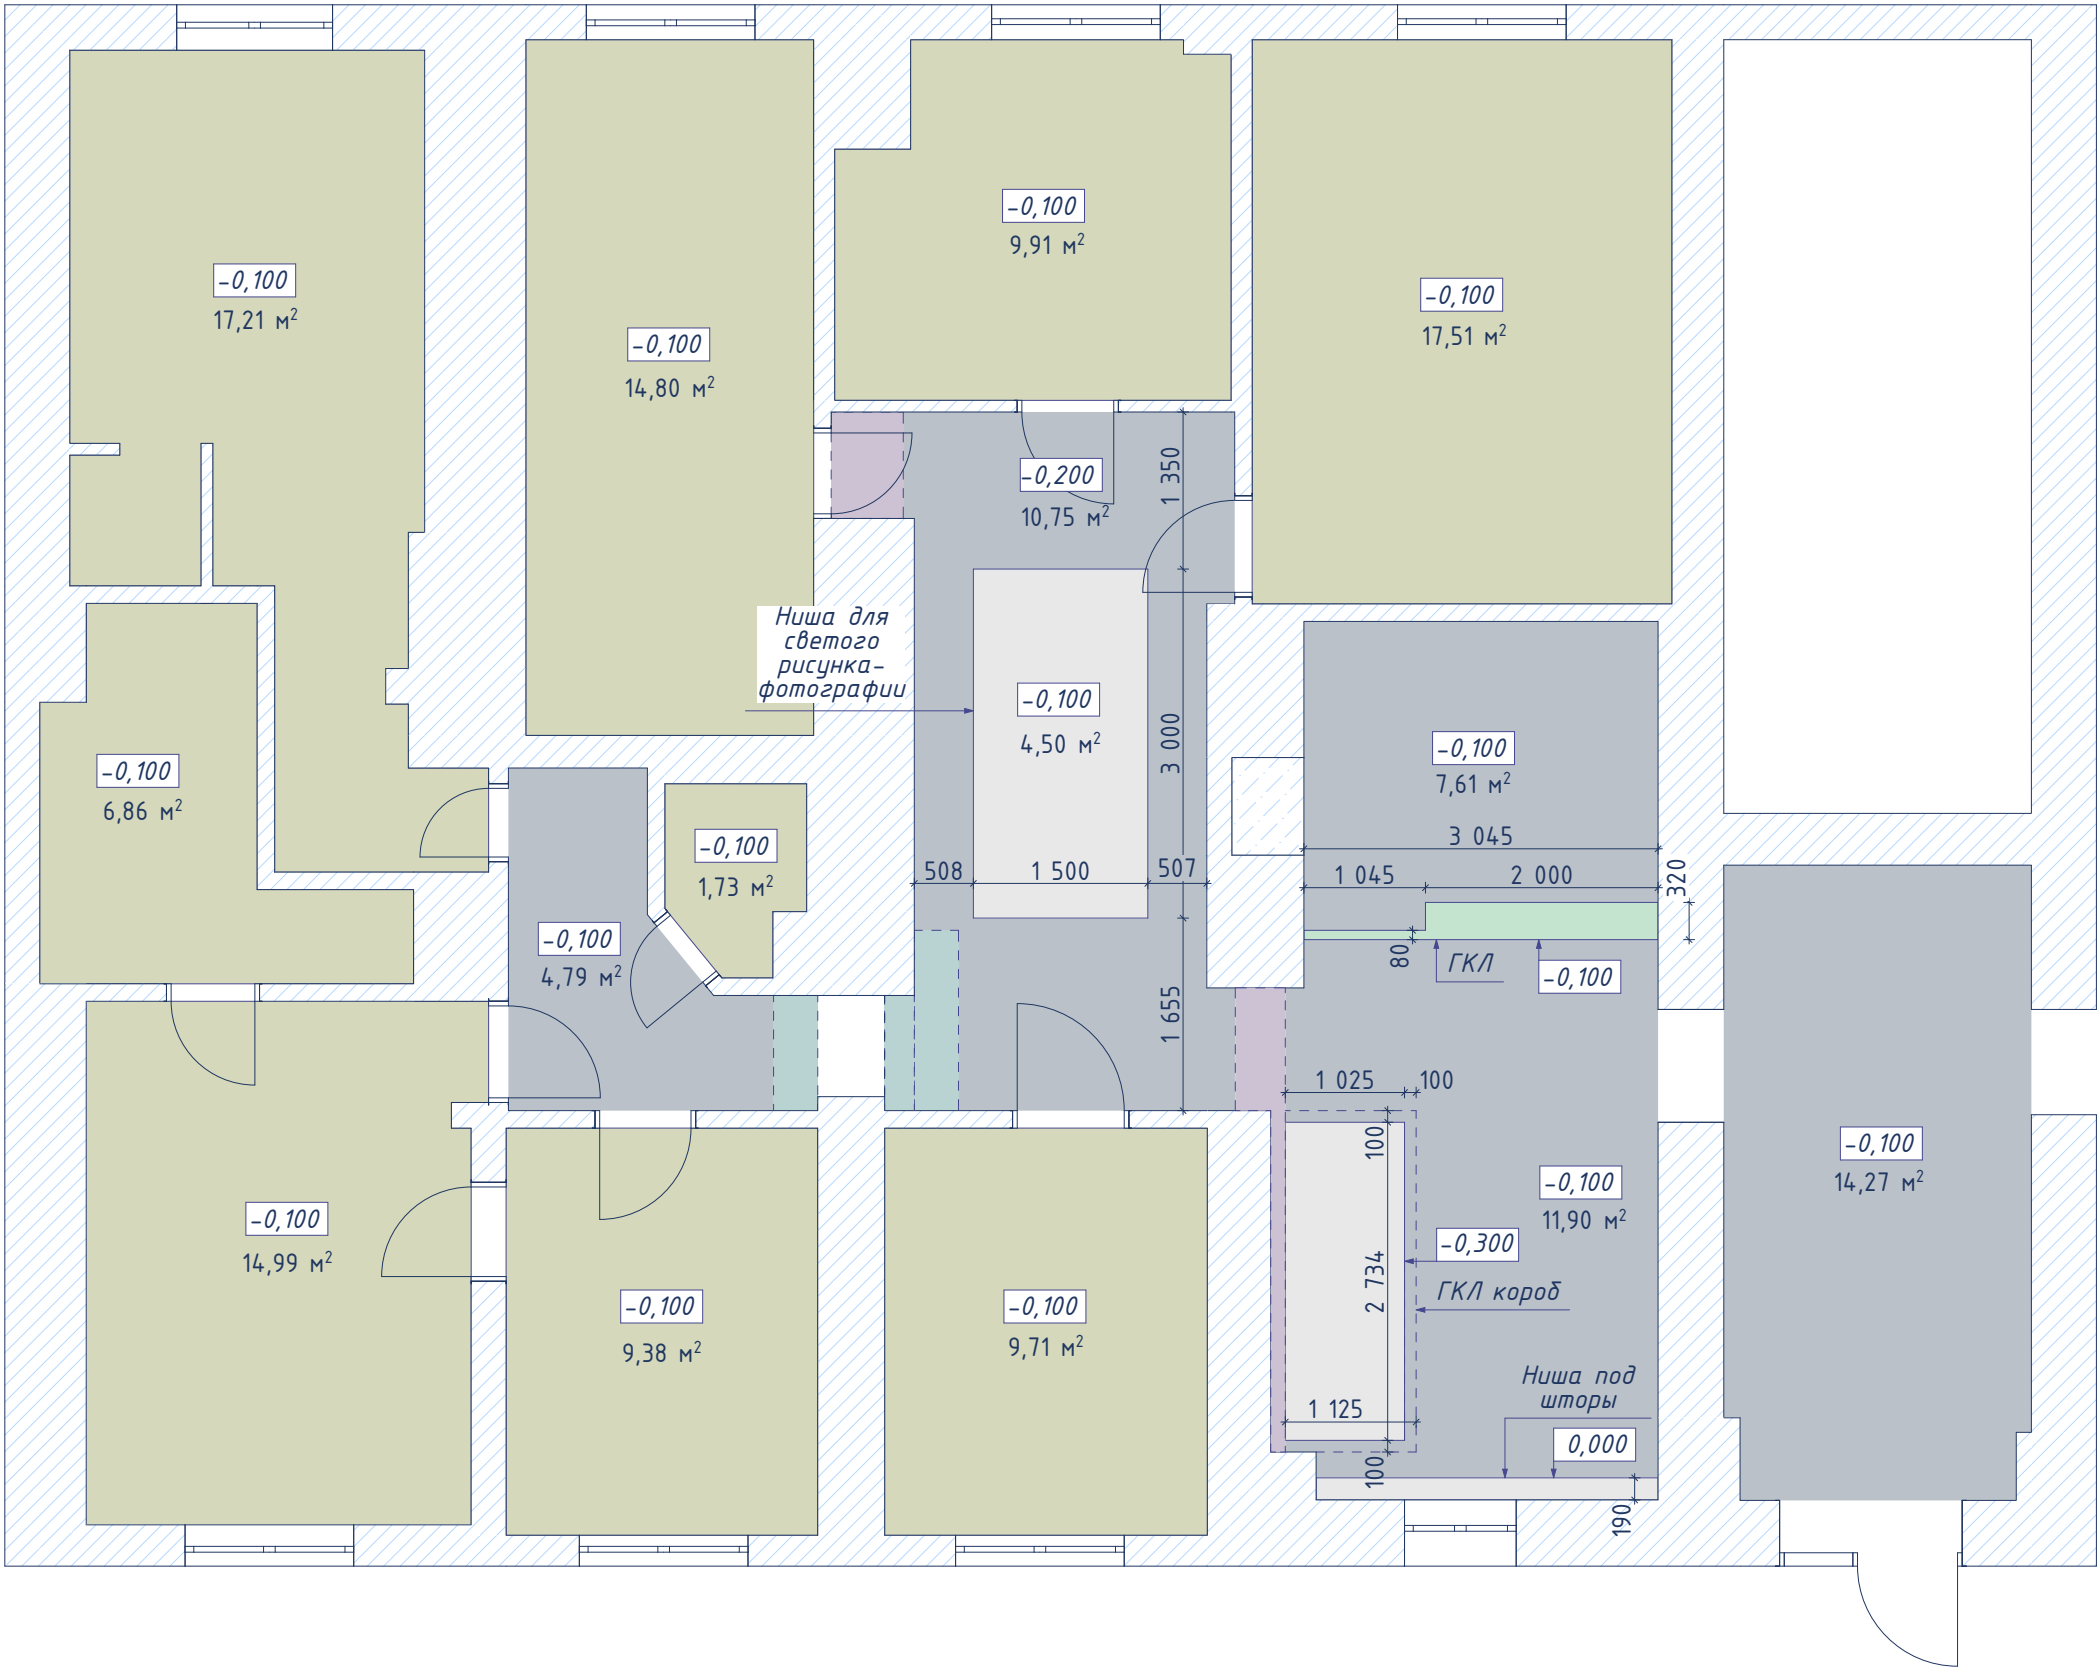

Разрез ГКЛ короба над шкафом

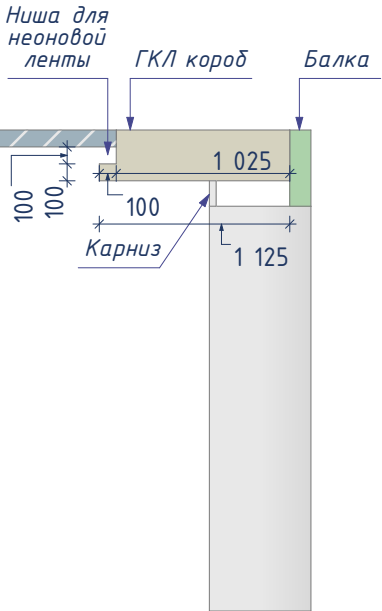


План размещения светильников левого крыла медицинского центра

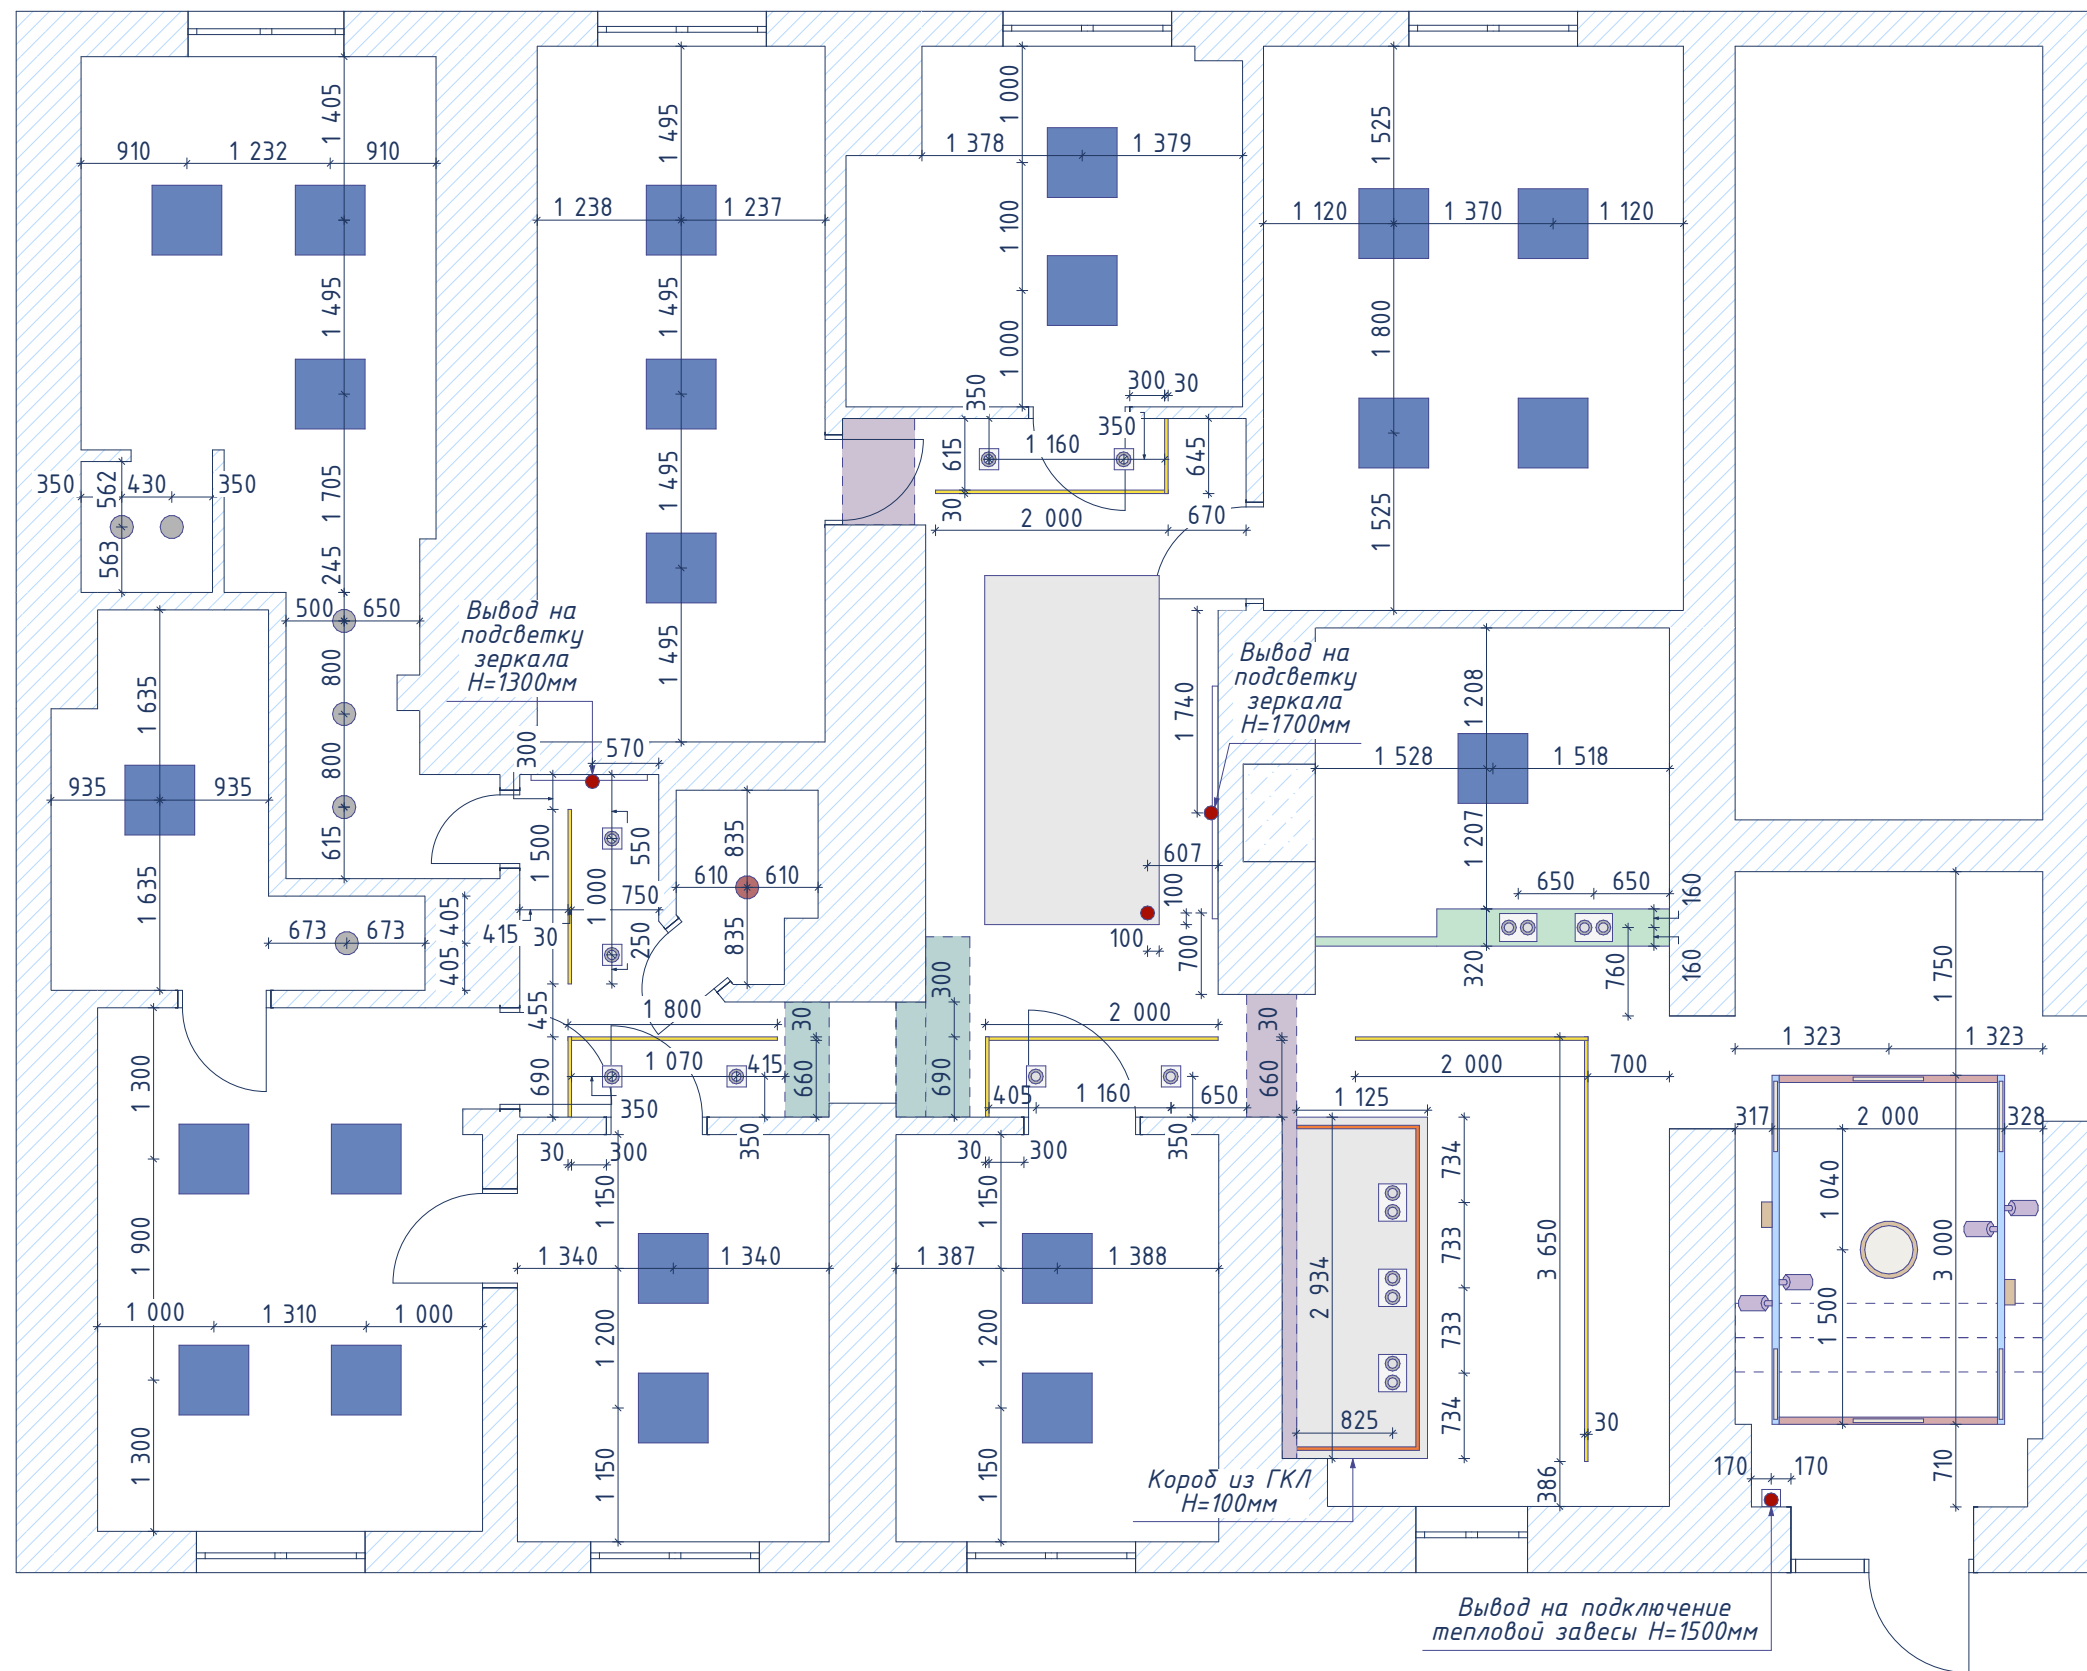

- Светодиодная панель DL-TITAN-S Day4000 Arlight 038426(1), 600x600мм, 21шт
- Светильник потолочный A6650PL-1WH FADO, 400мм, 1шт
- Подвесная люстра Lussole KNOX LSP-7416, 700мм, 1шт
- Светильник потолочный встраиваемый TARF A2168PL-2WH, 160x80мм, 6шт
- Точечный встраиваемый светильник Arte Lamp TARF A2168PL-1WH, 92x92x22мм, 8шт
- Линейный светильник
- Подсветка светодиодная лента
- Шинопровод встраиваемый LINEA A4 73333, 3000x62мм, 2шт
- Шинопровод встраиваемый LINEA A4 72233, 2000x62мм, 2шт
- Светильник потолочный LINEA A4 693PL-1WH, 605x22x43мм, 6шт
- Светильник потолочный LINEA A4 693PL-1WH, 127x60x230мм, 4шт
- Светильник потолочный LINEA A4 696PL-1WH, 127x60x230мм, 2шт
- Вывод на подключение
- Светильники из наличия

План левого крыла медицинского центра с привязками выключателей и указанием включения групп светильников

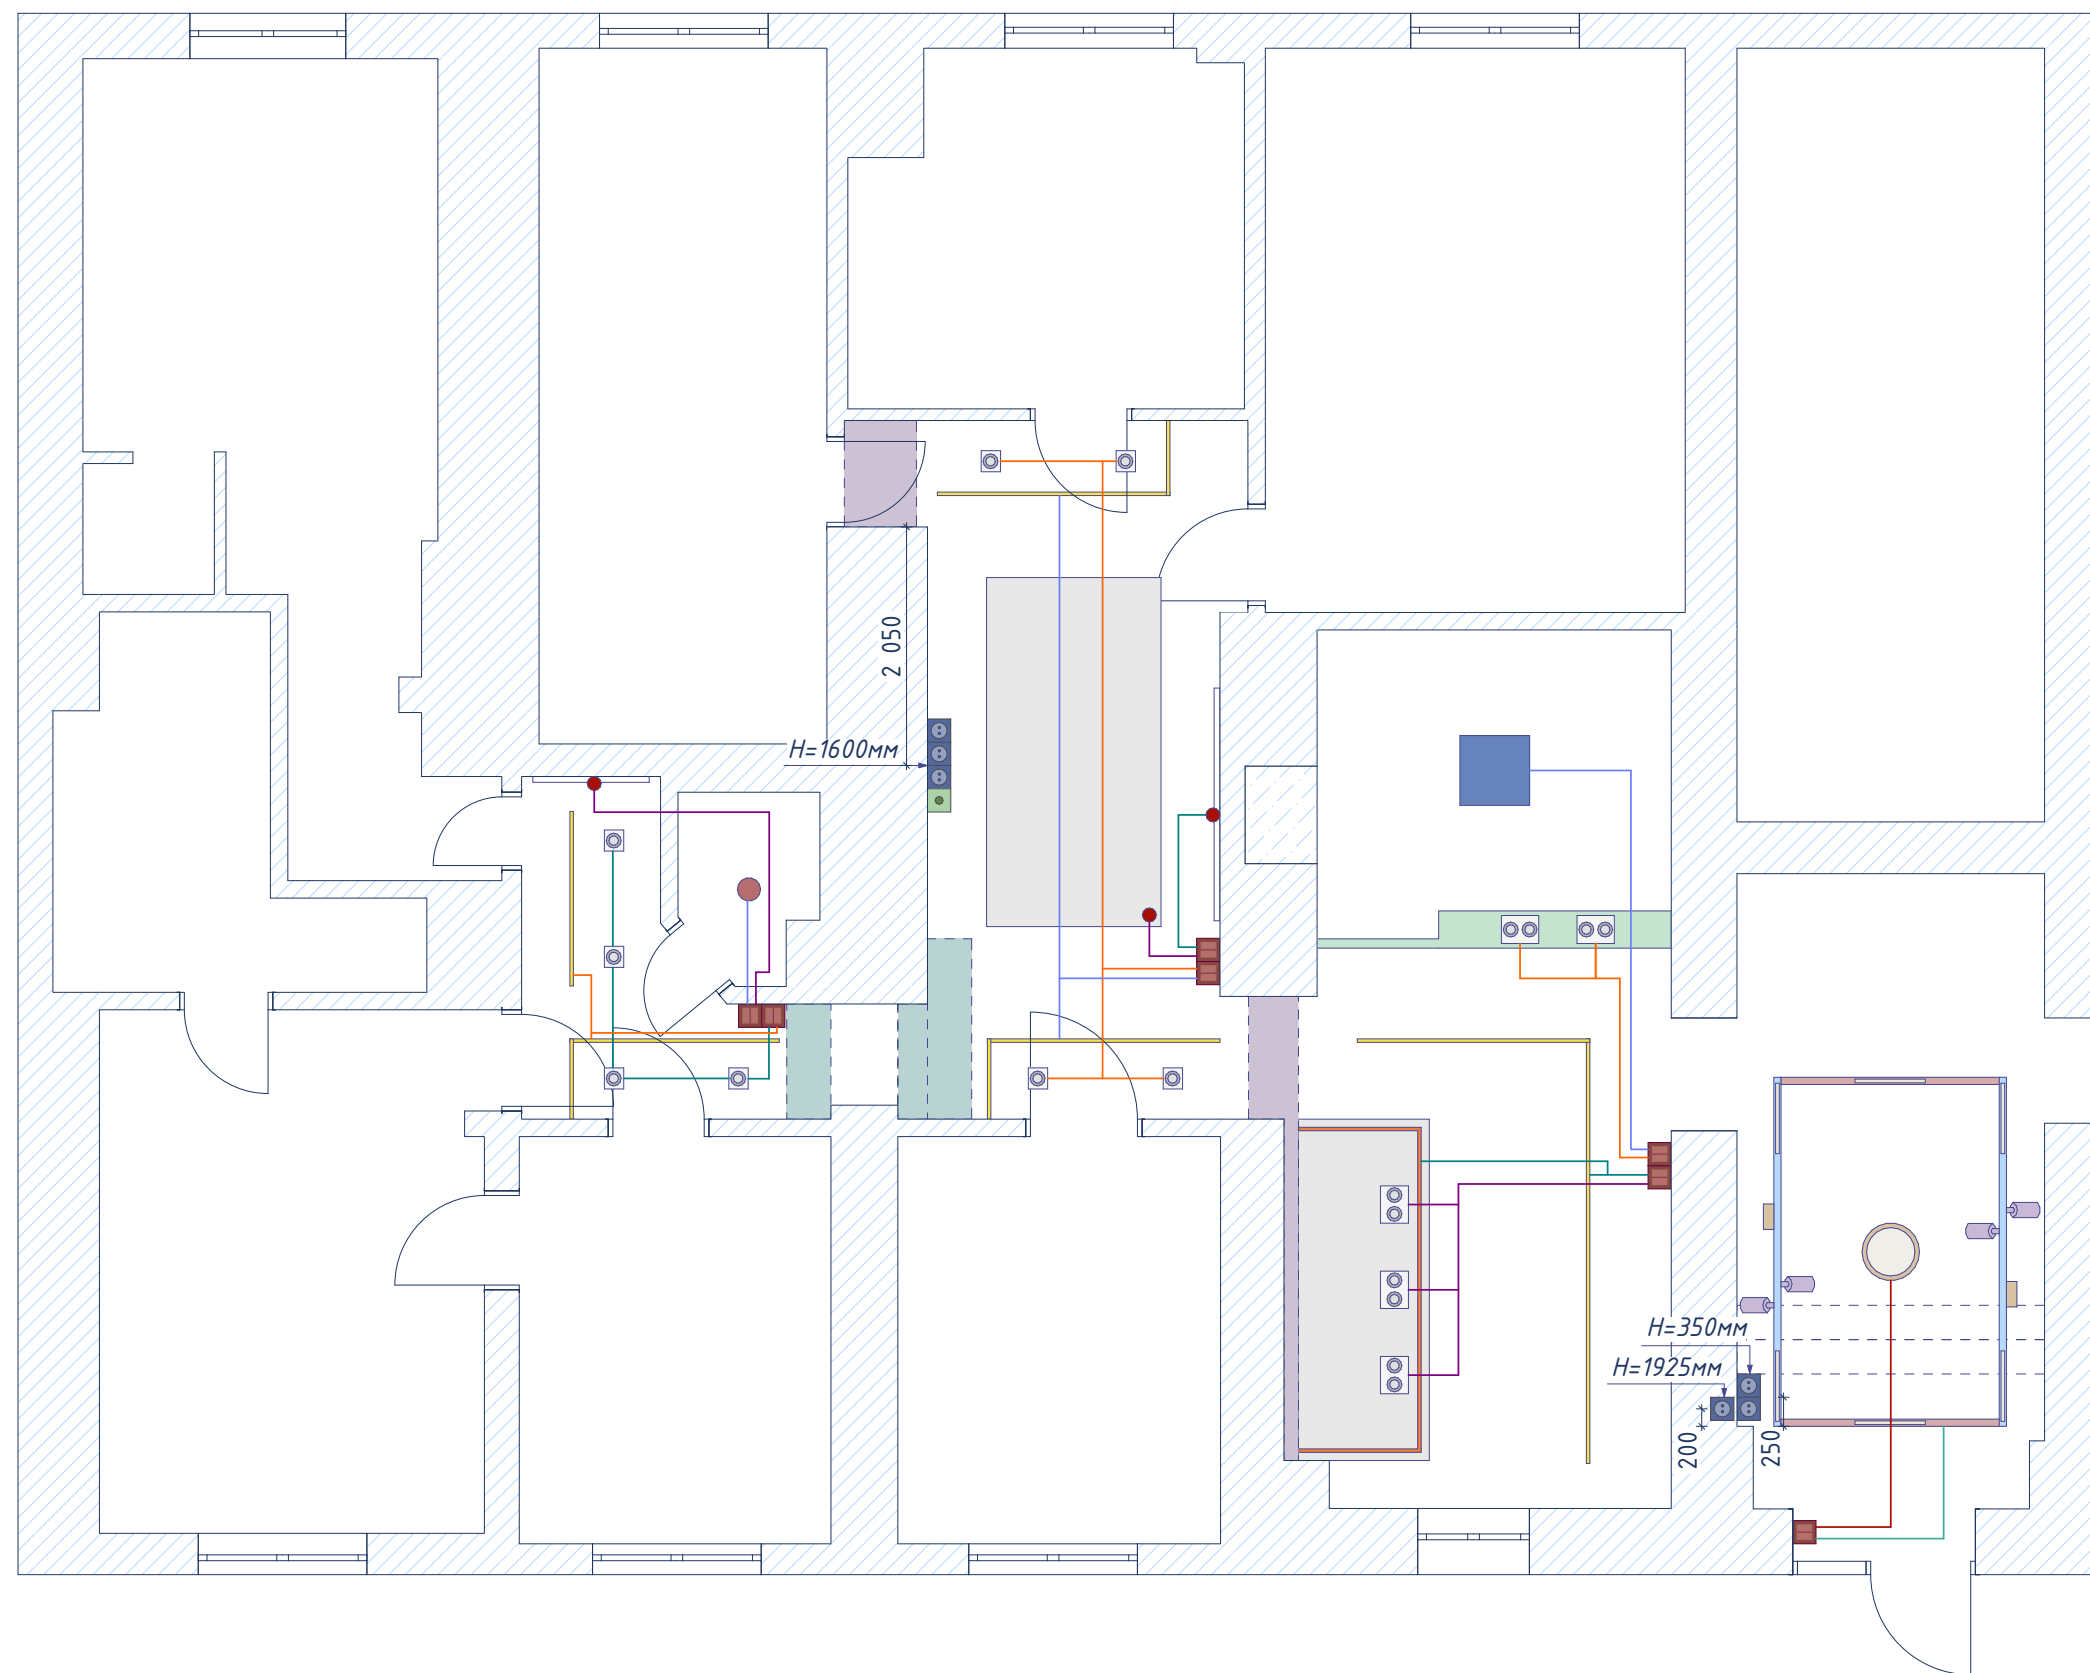

-  - Выключатель (2-ух клавишный)
-  - Розетка
-  - Розетка ТВ


Примечания:

Все выключатели расположить на высоте уже существующих выключателей


План маркировок левого крыла медицинского центра




План правого крыла медицинского центра после перепланировки

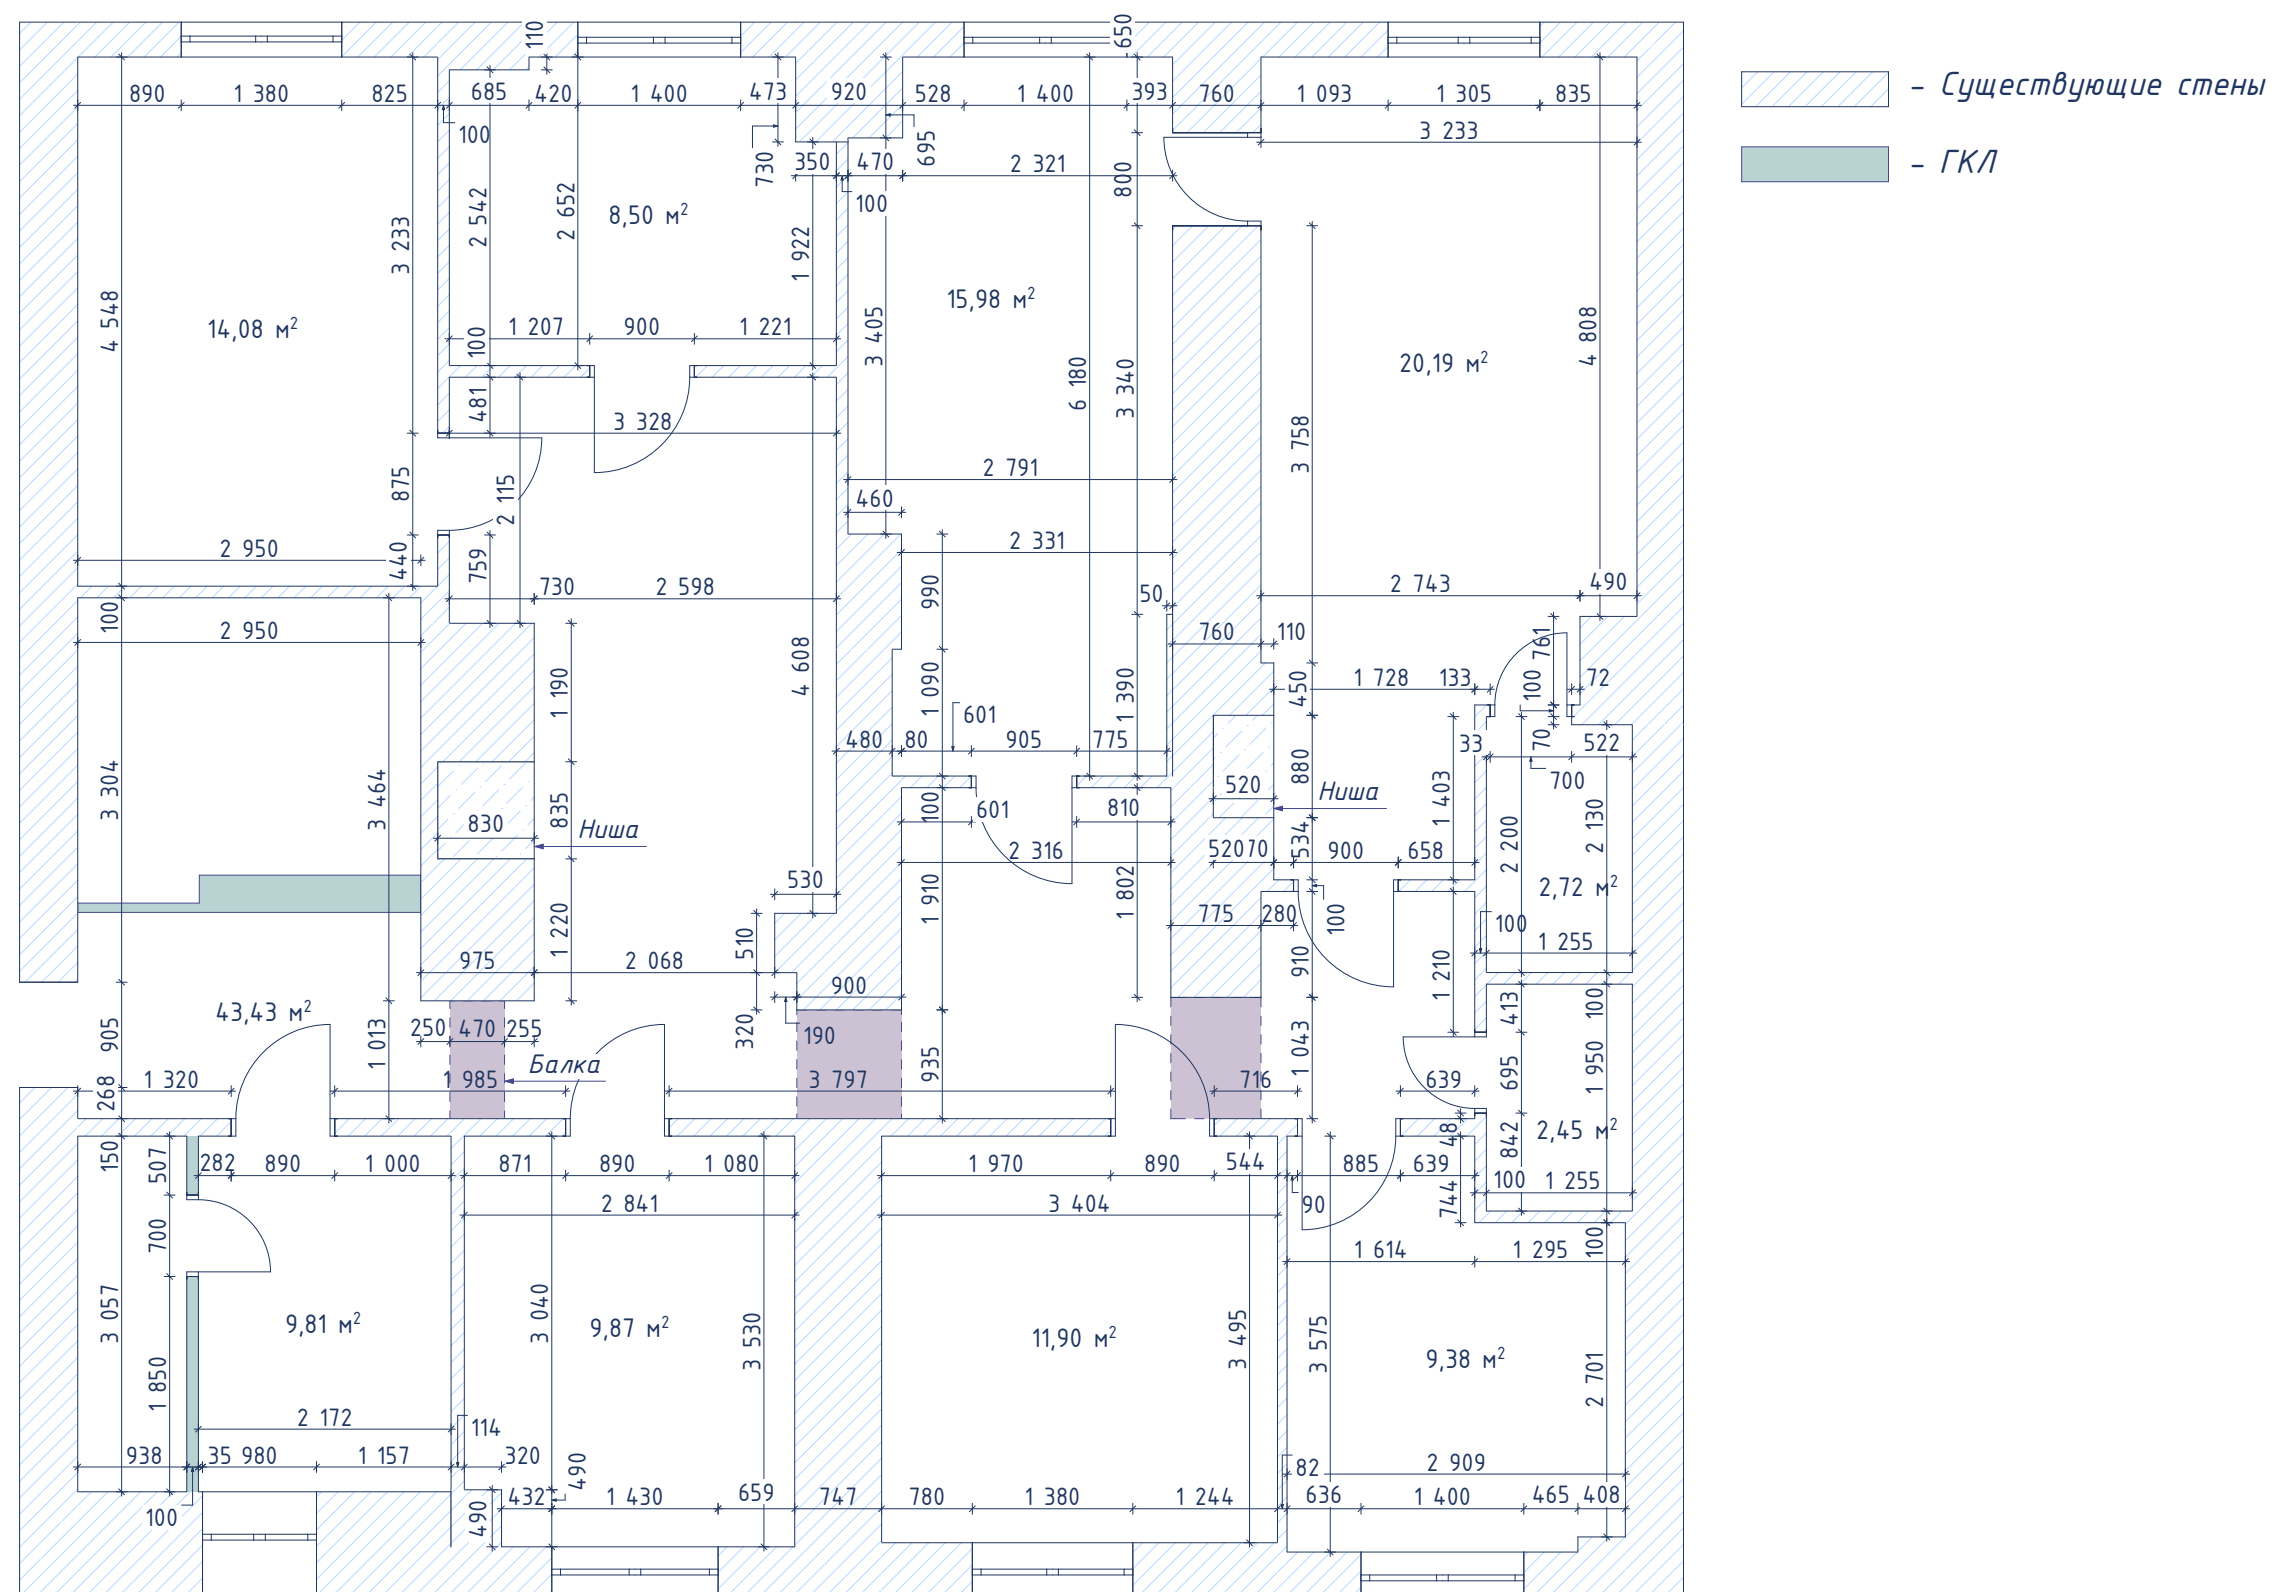


План потолков правого крыла медицинского центра

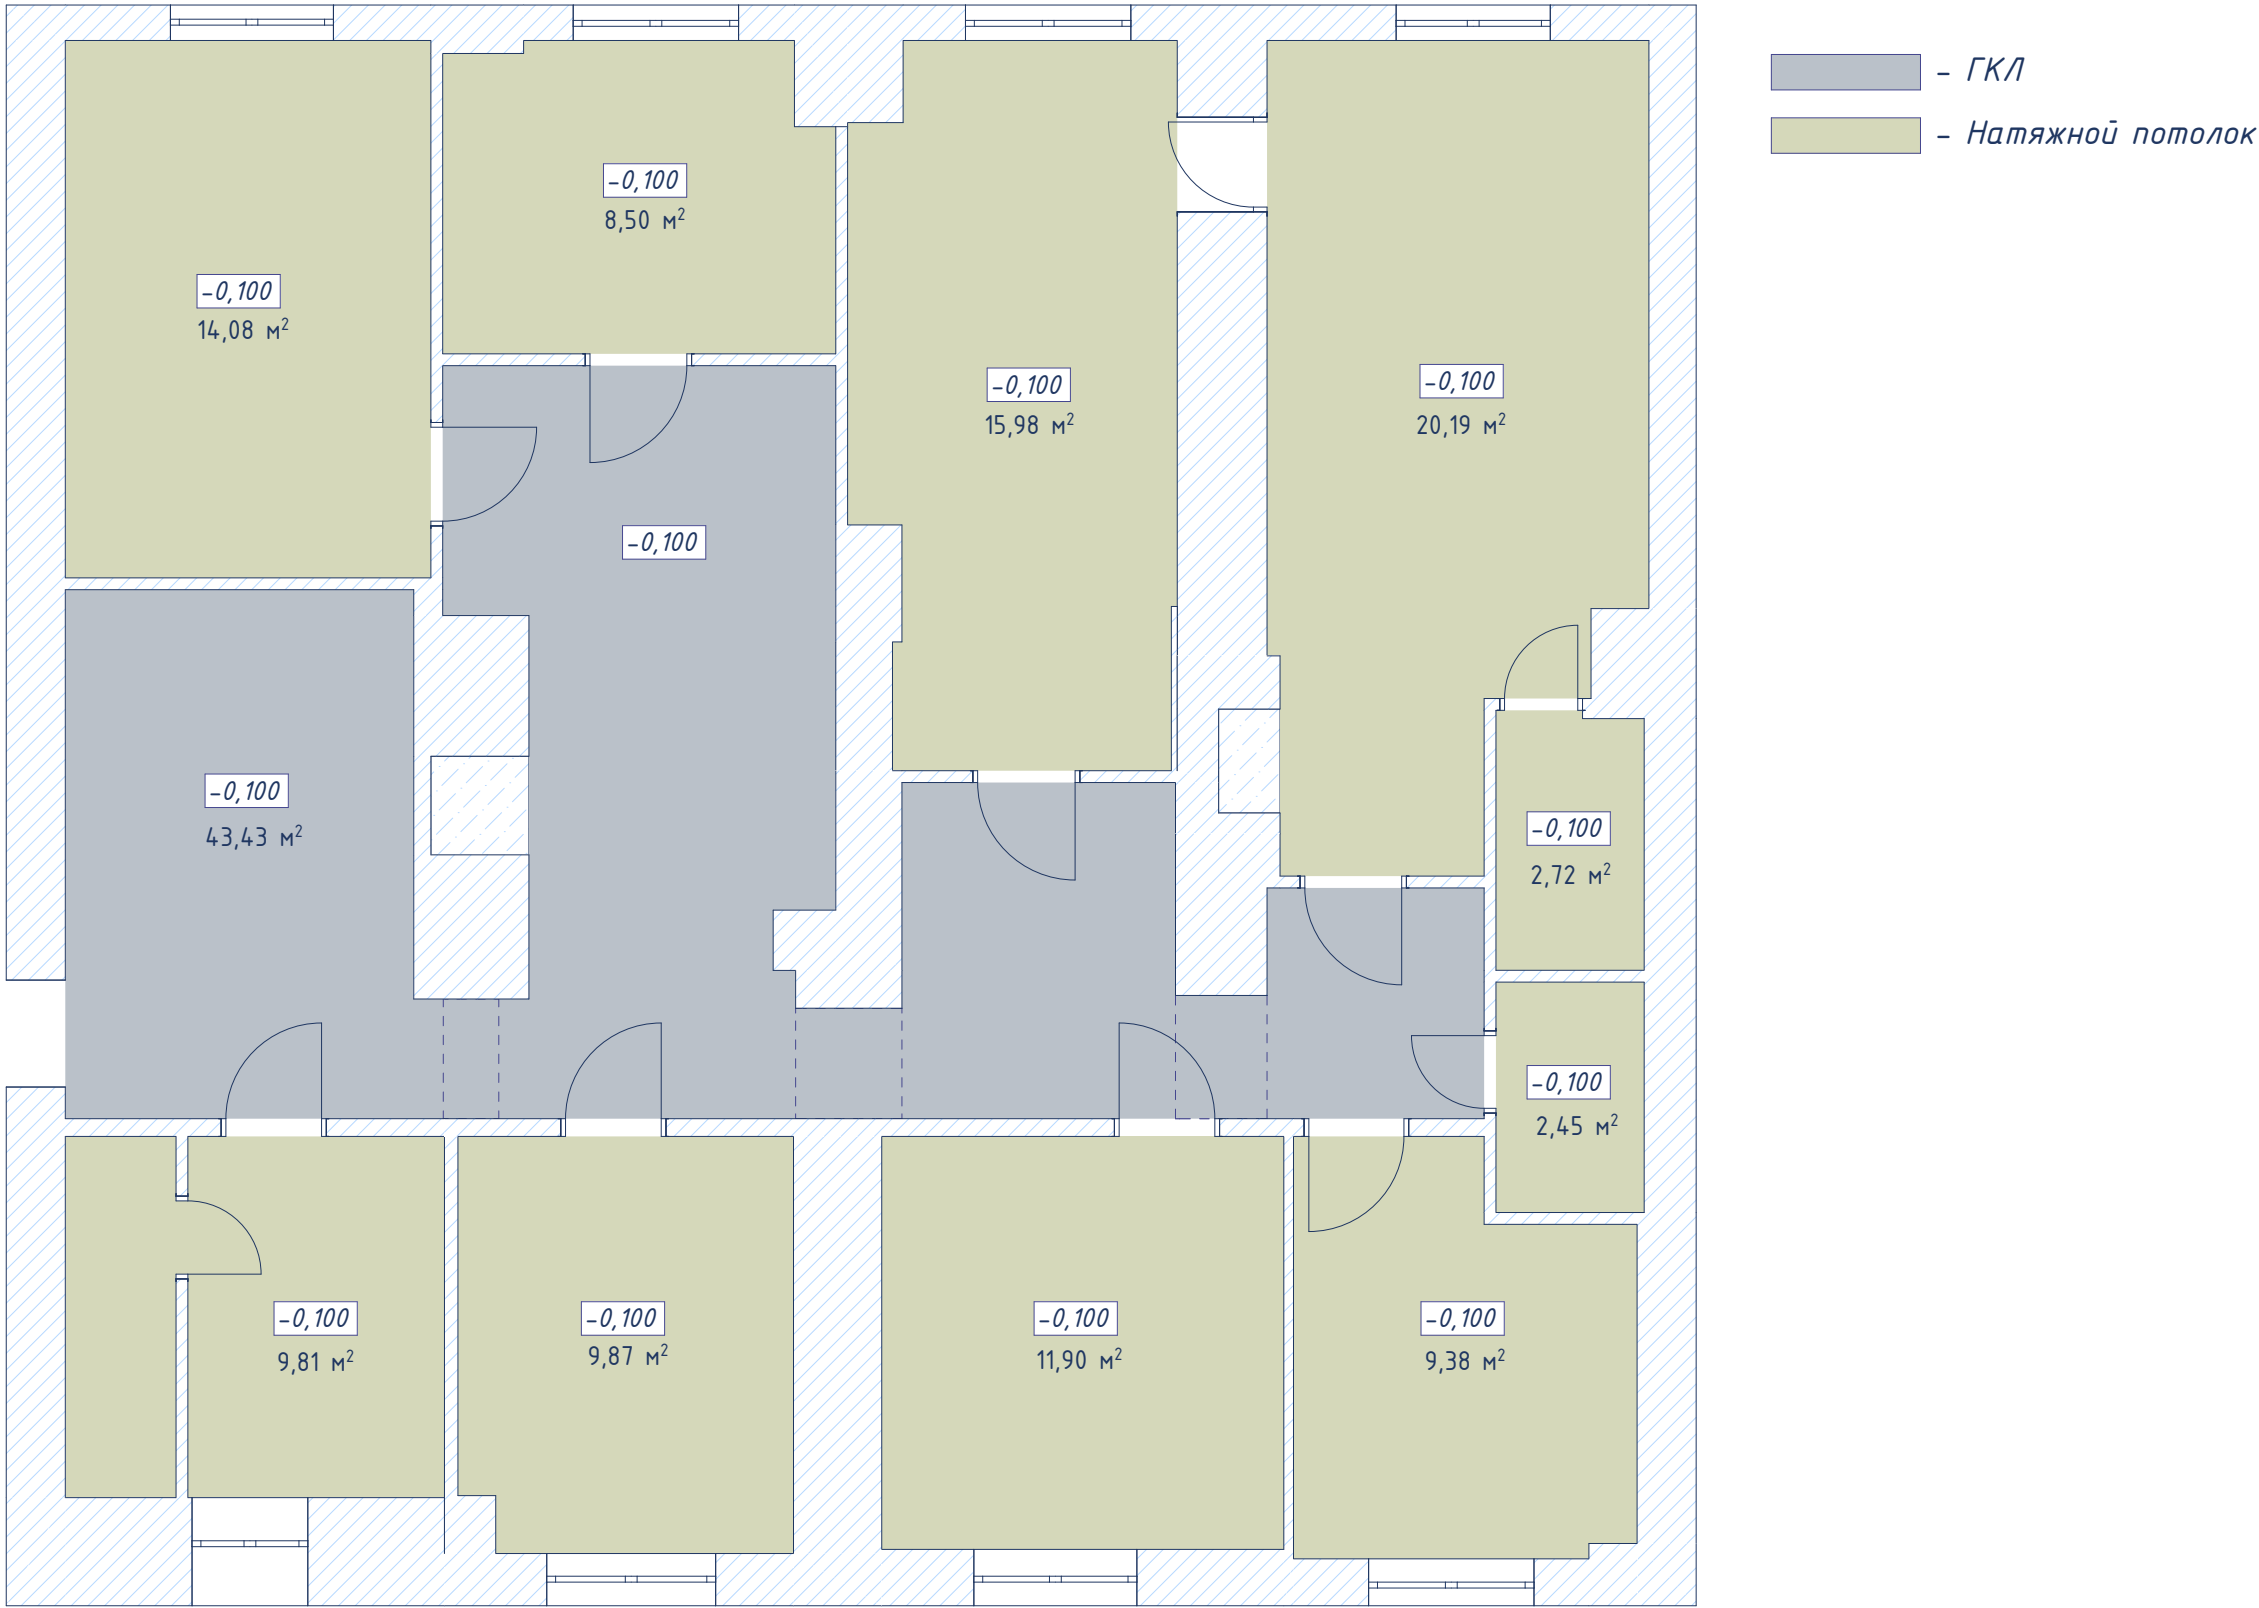



План размещения светильников правого крыла медицинского центра

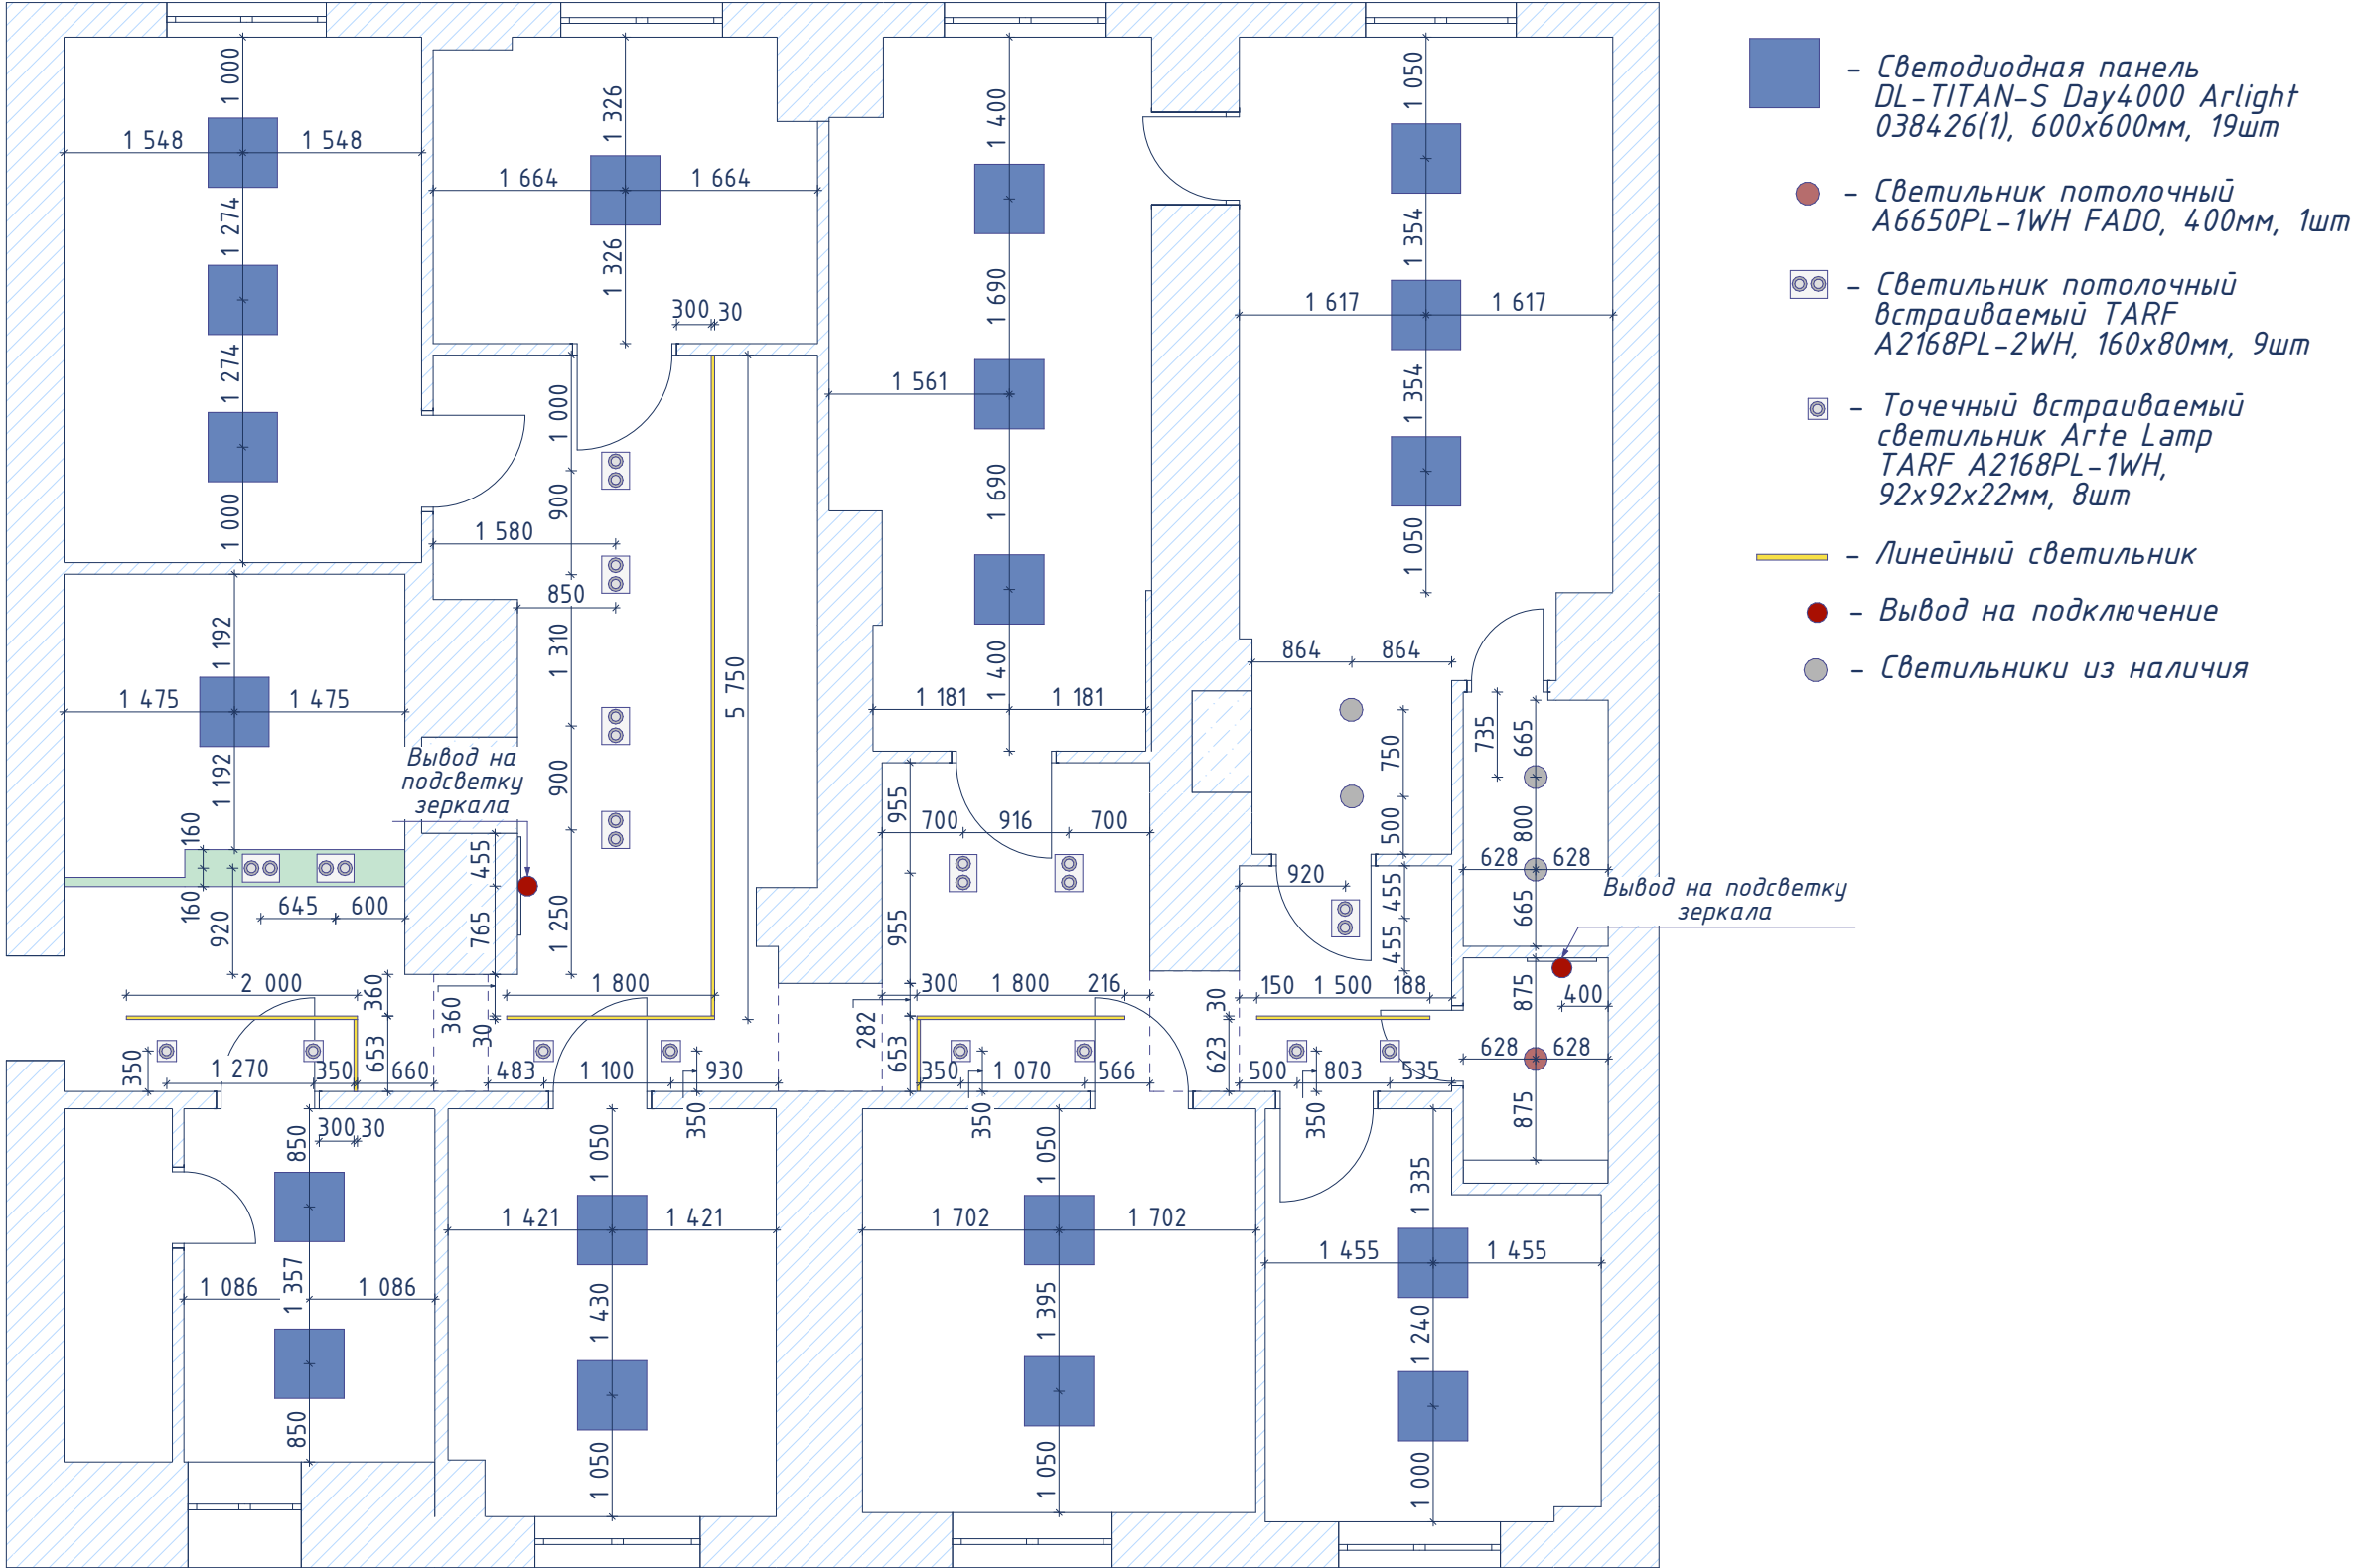

План маркировок правого крыла медицинского центра

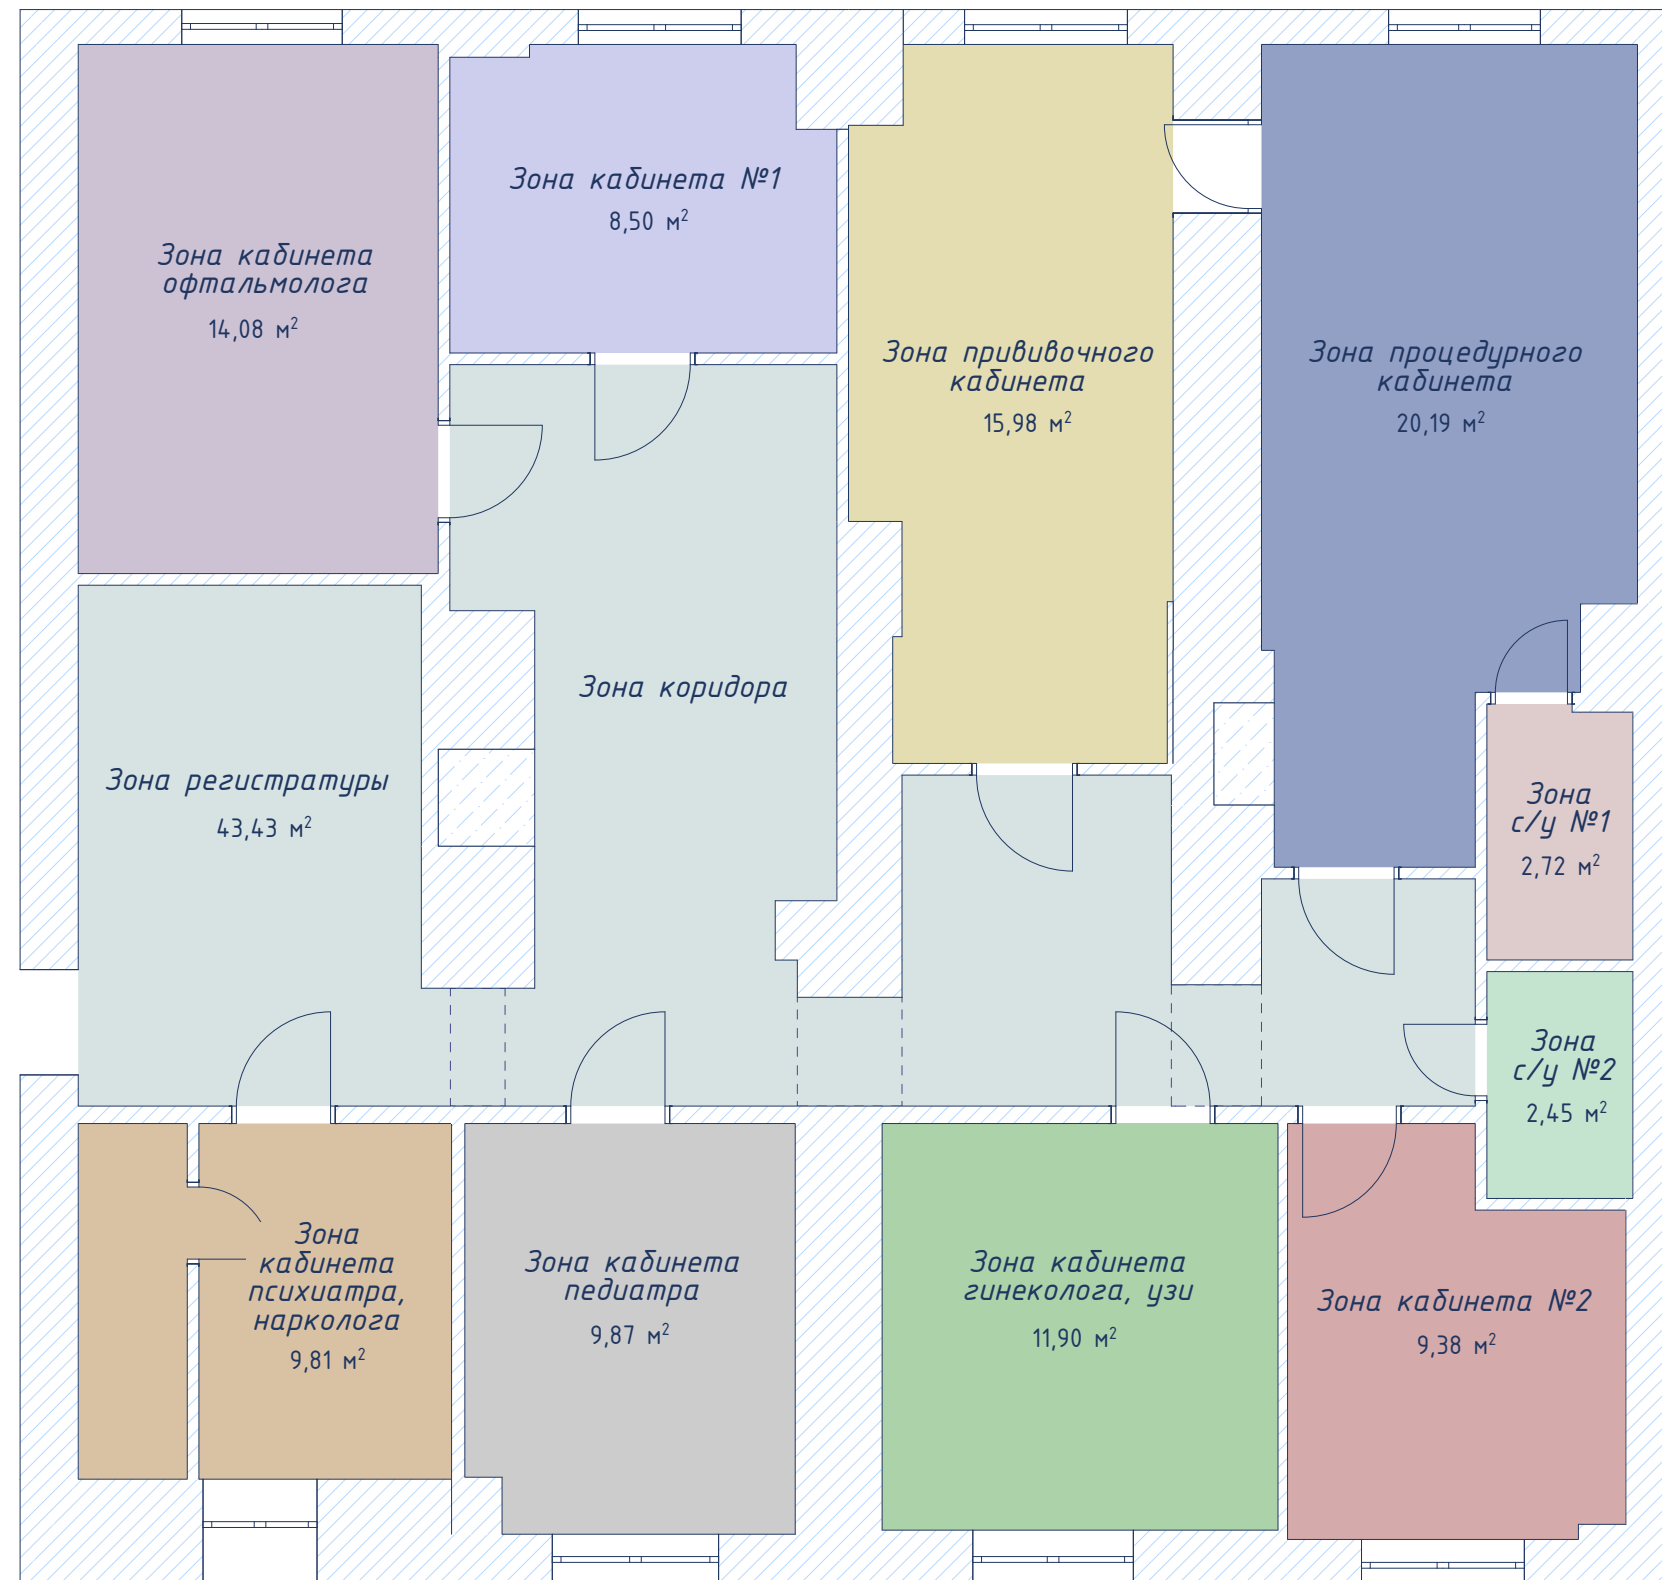





Развертки зоны входа

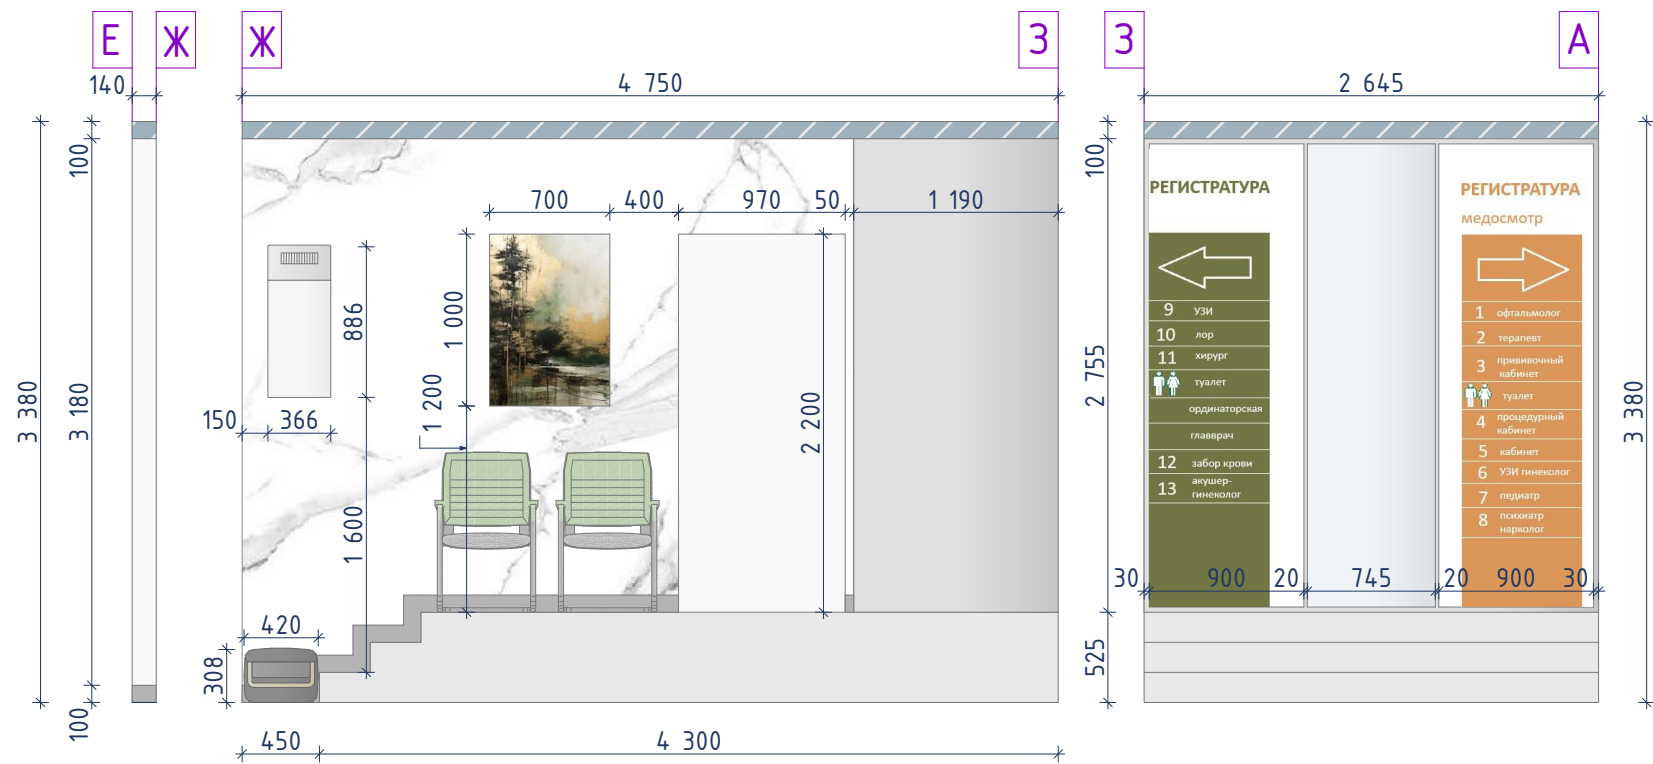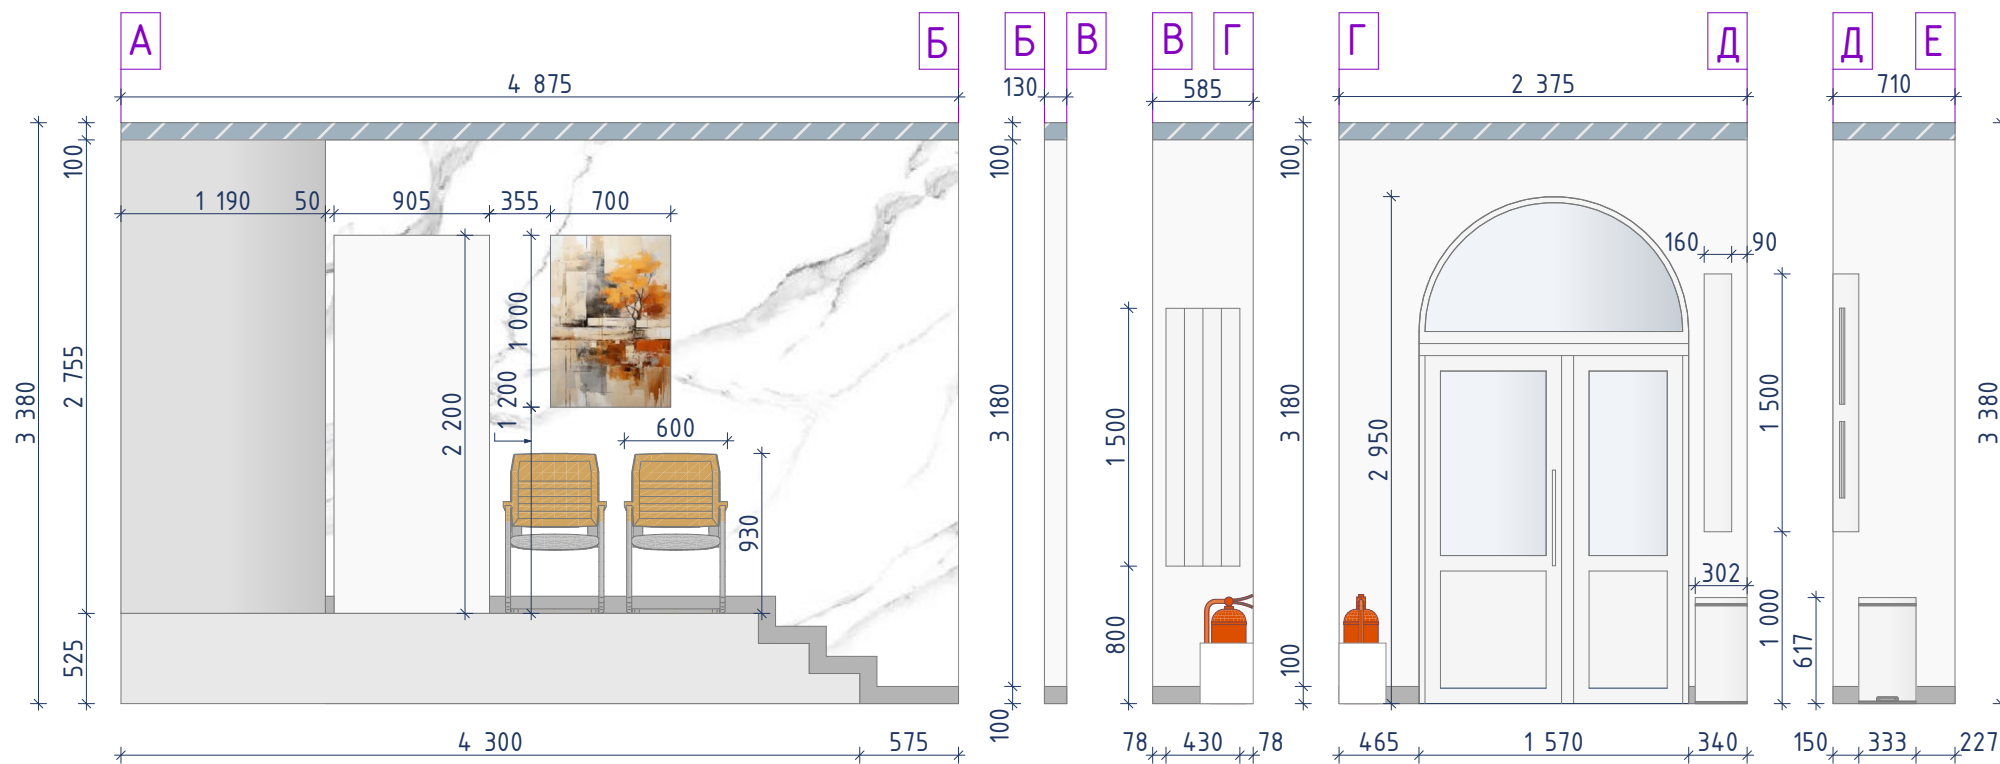

-  - Натяжной потолок белый
-  - Алюминиевый плинтус ECO GBPLAS 100


Развертки зоны регистратуры

Стойка регистратуры

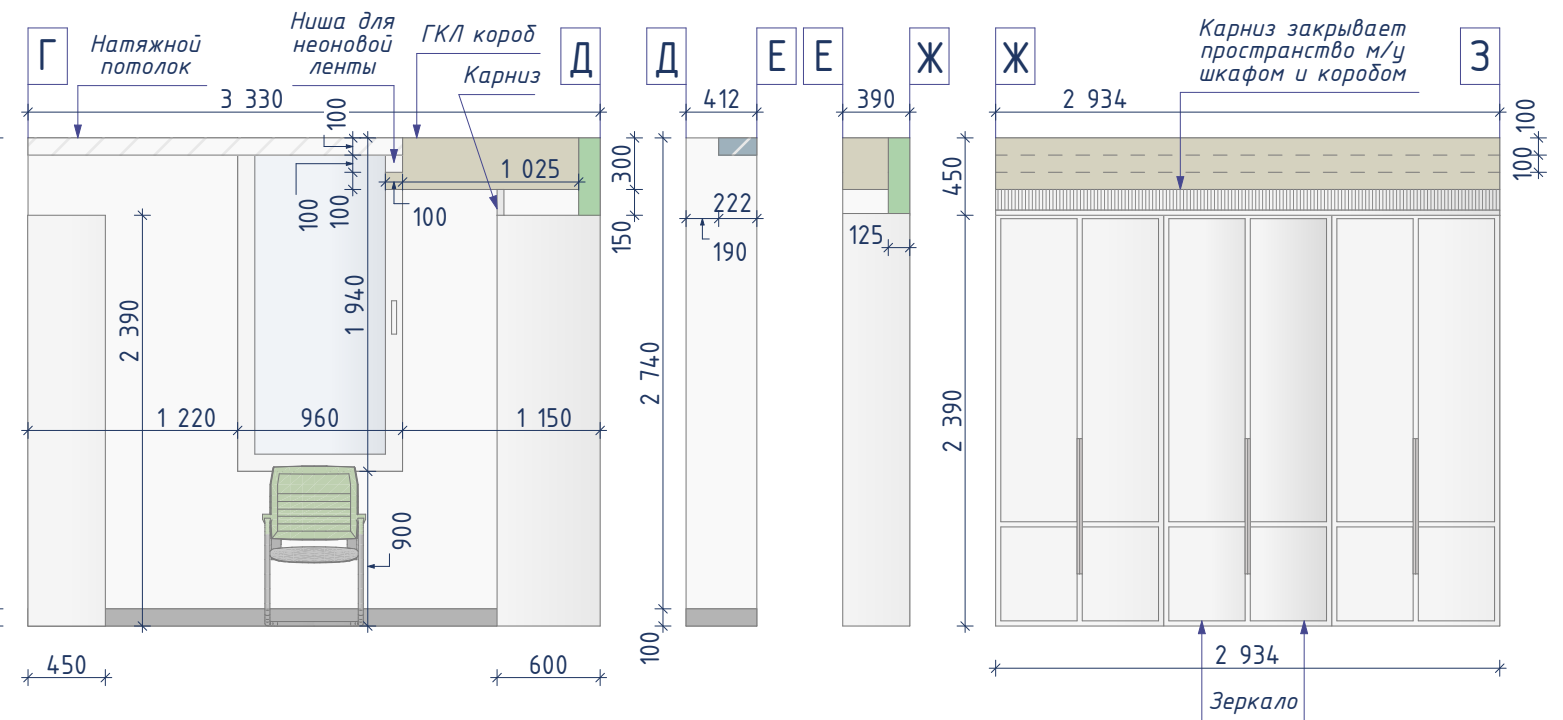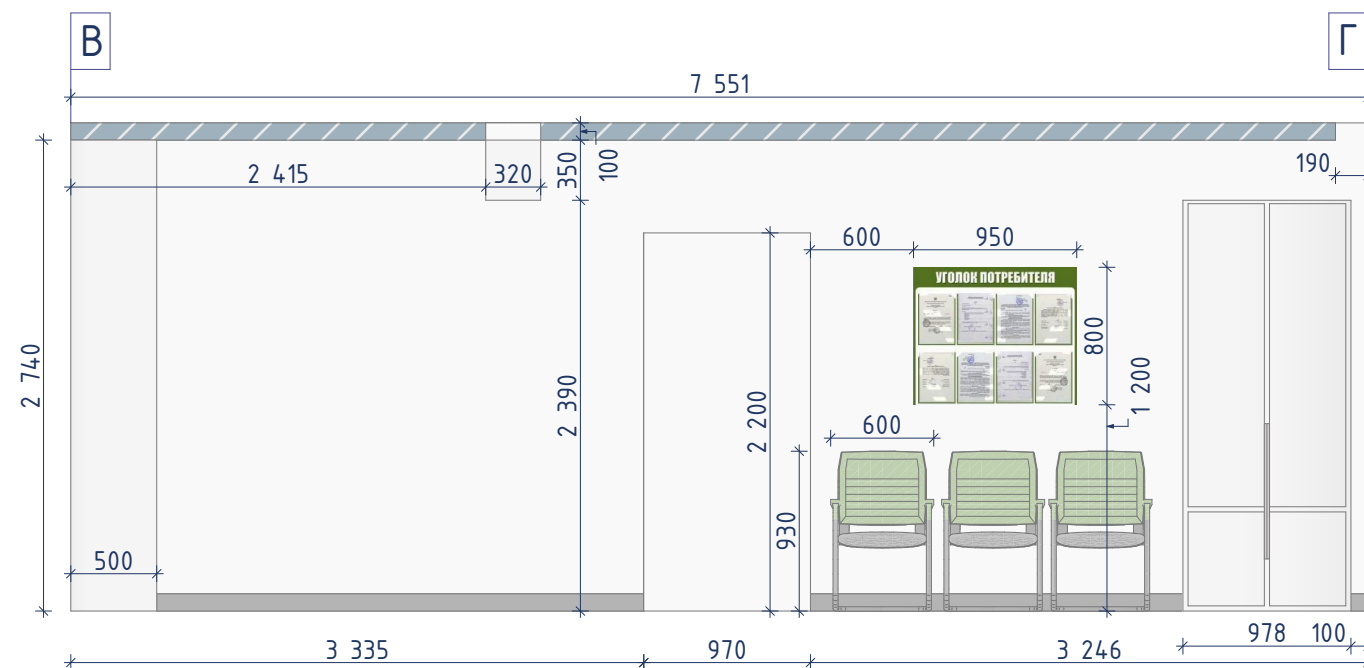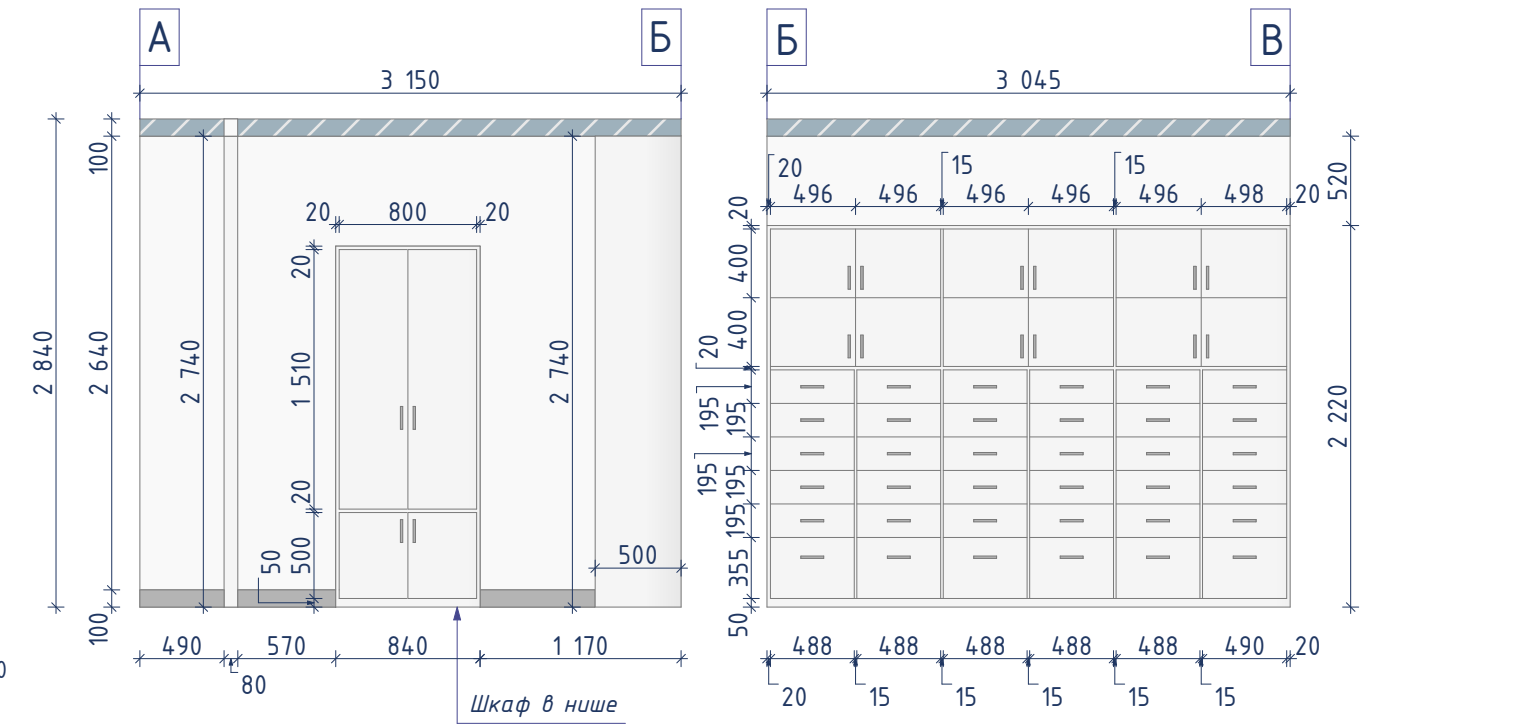
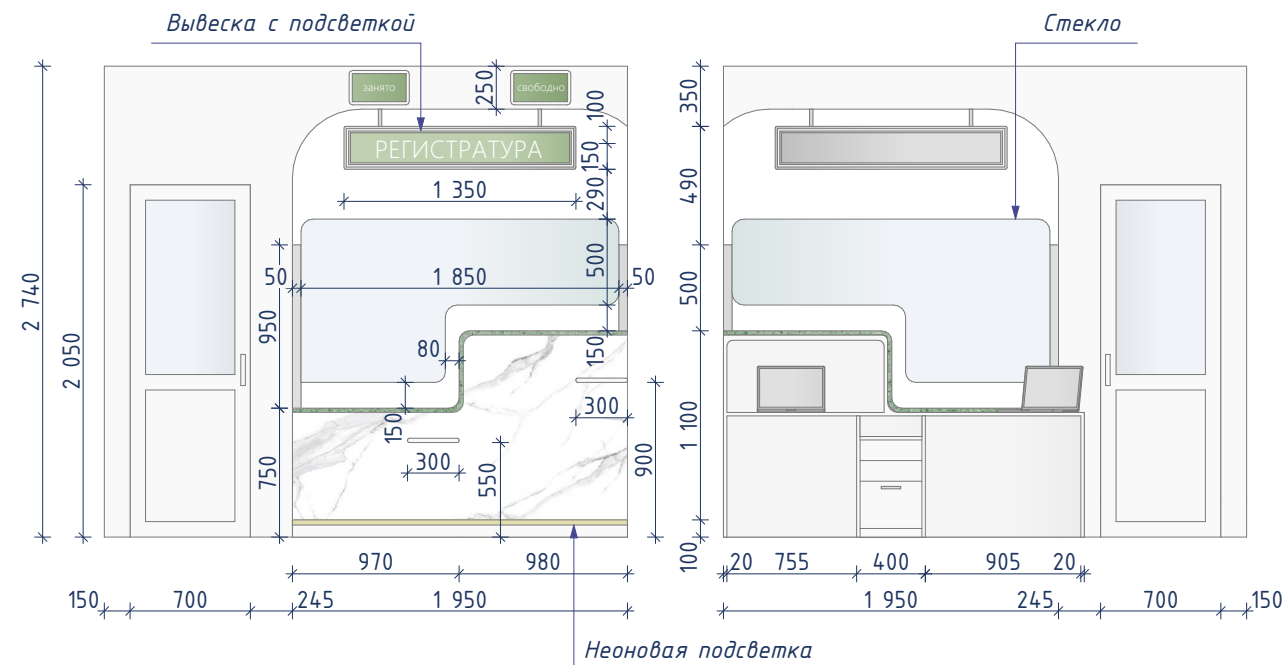


-  - Натяжной потолок белый (Stretch ceiling white)
-  - Алюминиевый плинтус ECO GBPLAS 100 (Aluminum baseboard ECO GBPLAS 100)

Развертки зоны коридора №1

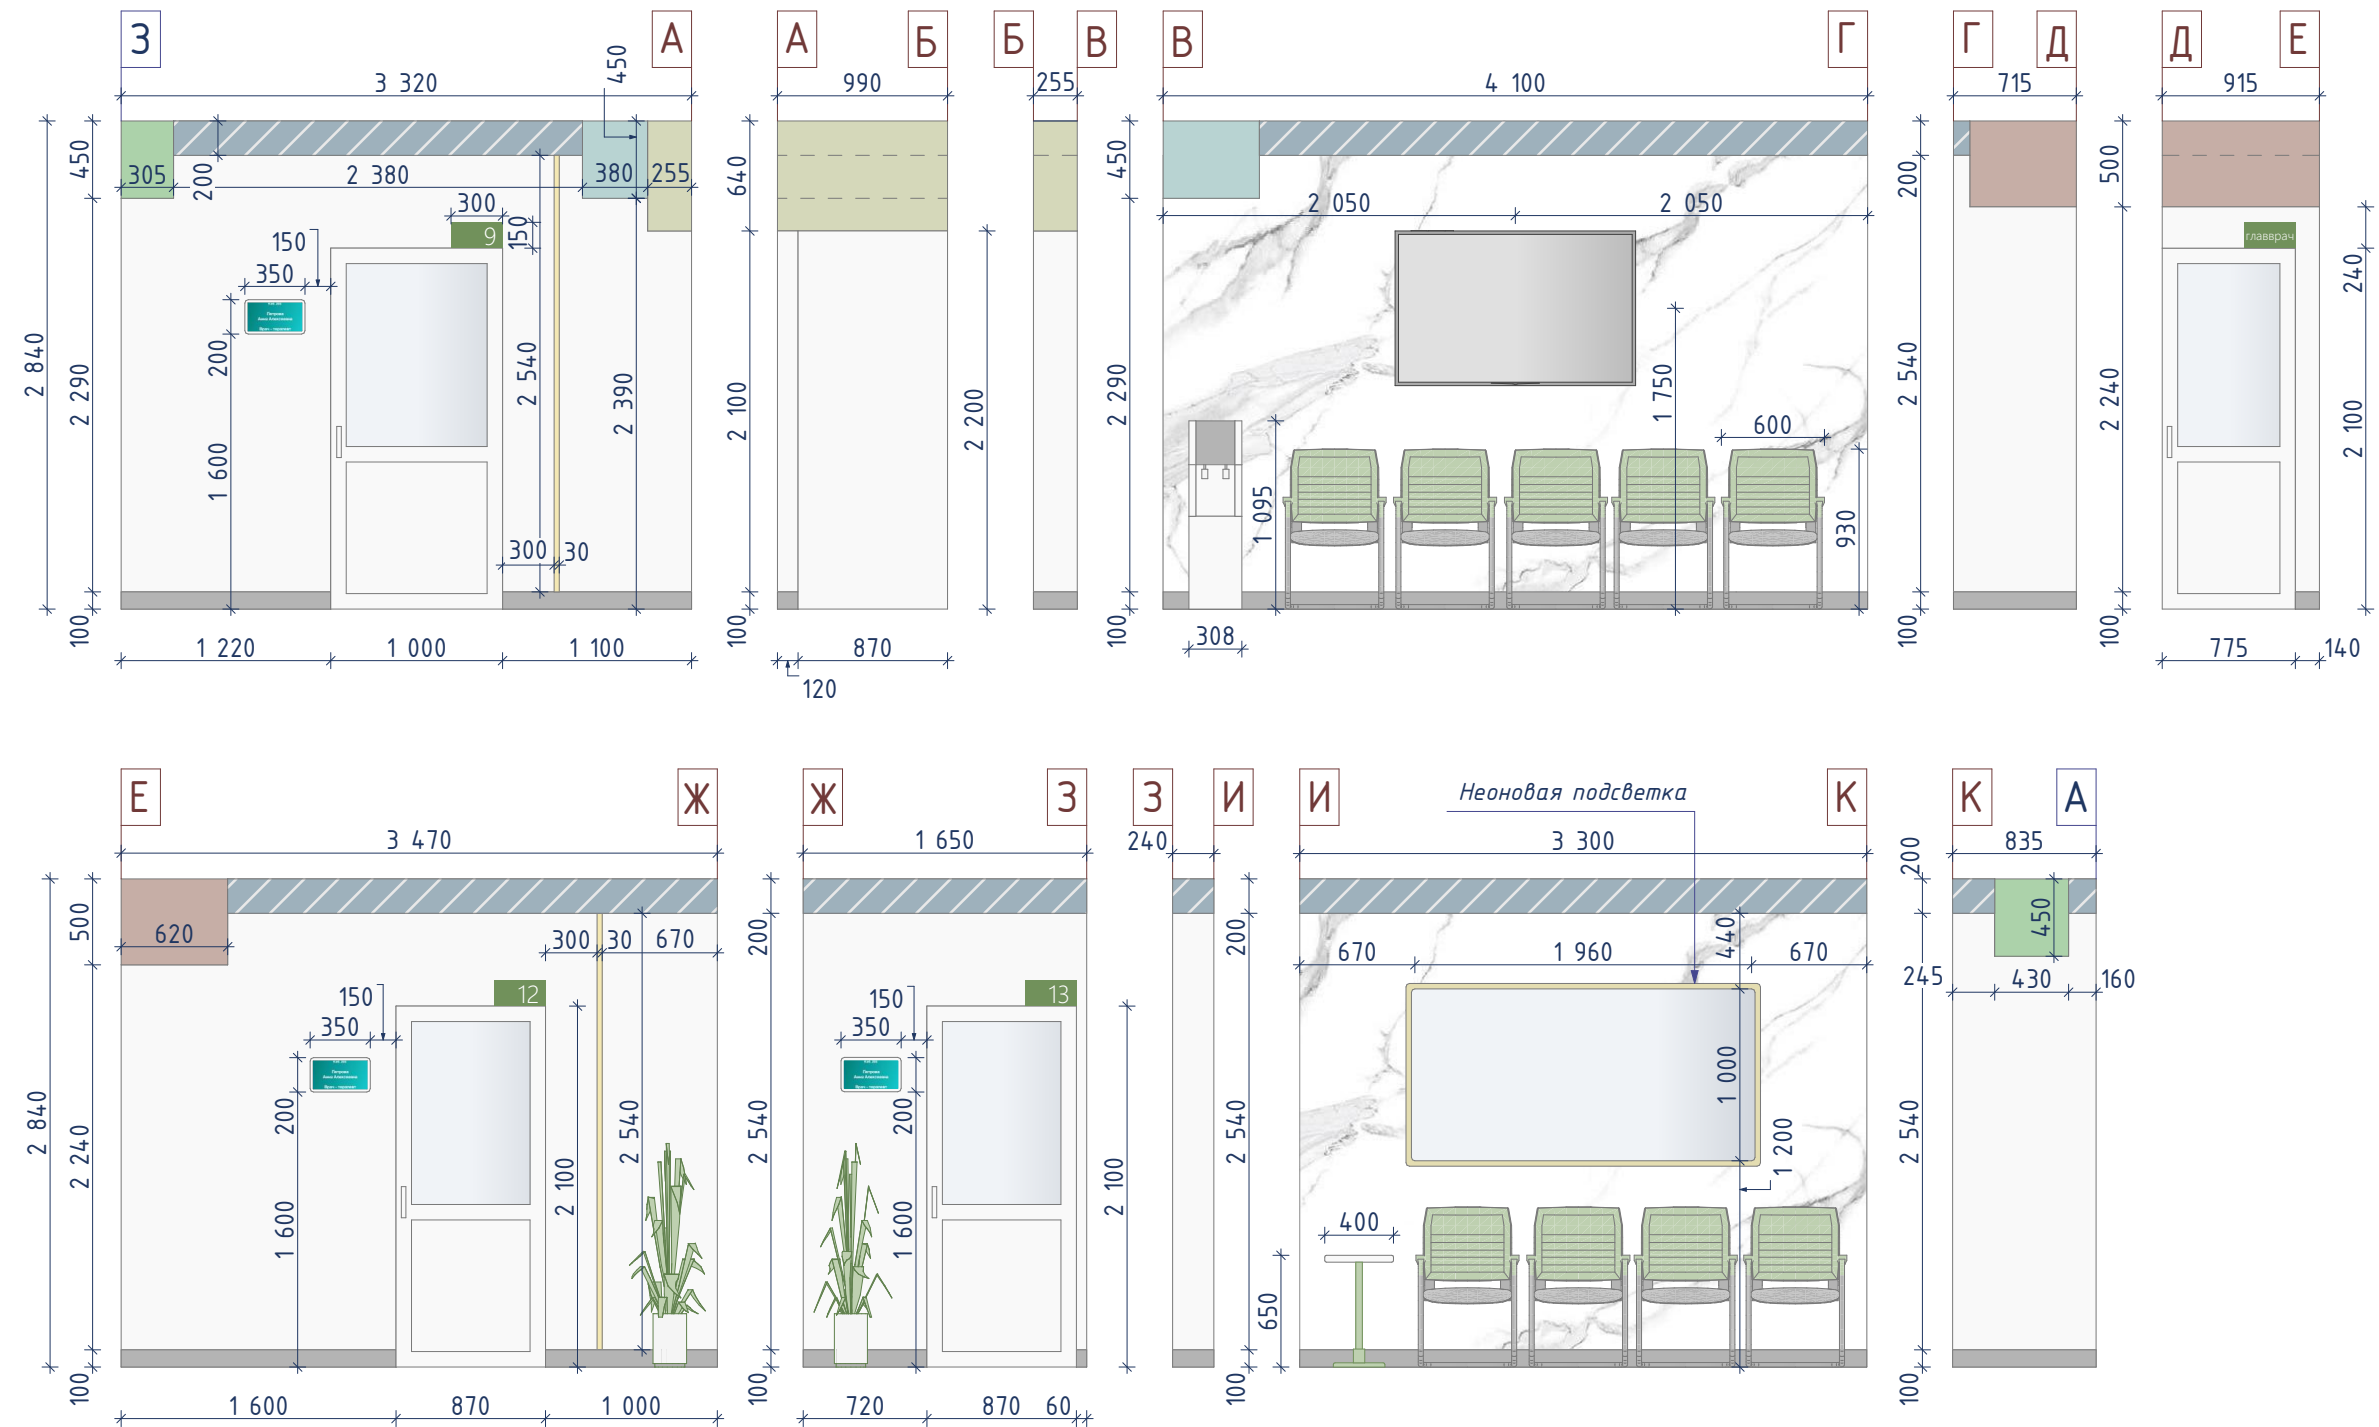

Развертки зоны коридора №2

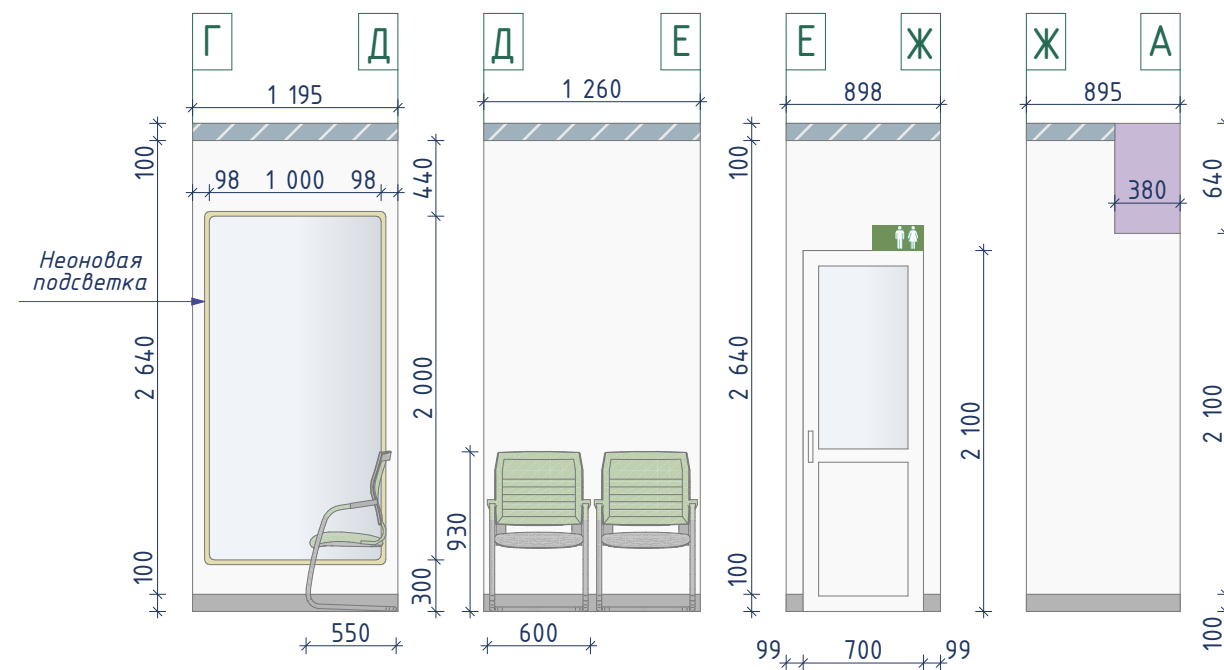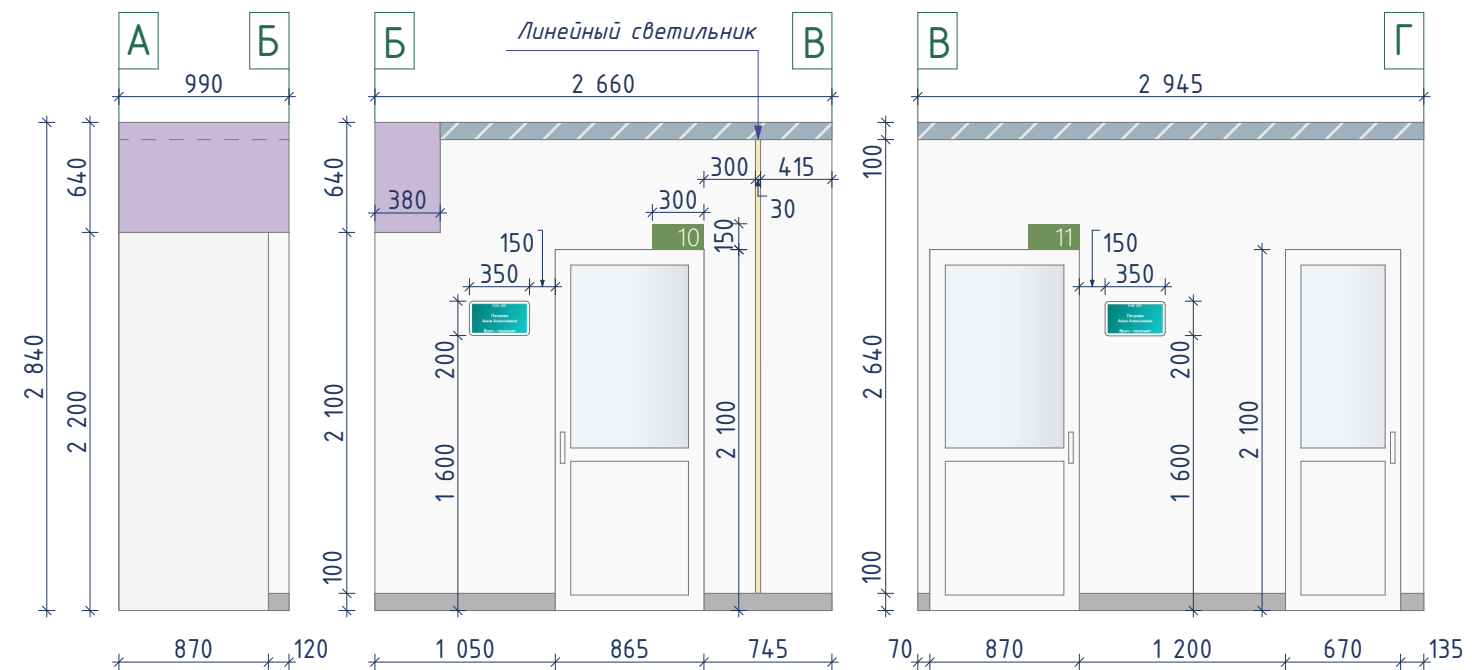

-  - Натяжной потолок белый
-  - Алюминиевый плинтус ECO GBPLAS 100

3Д картинки левого крыла медицинского центра




3Д картинки левого крыла медицинского центра




3Д картинки левого крыла медицинского центра



3Д картинки левого крыла медицинского центра

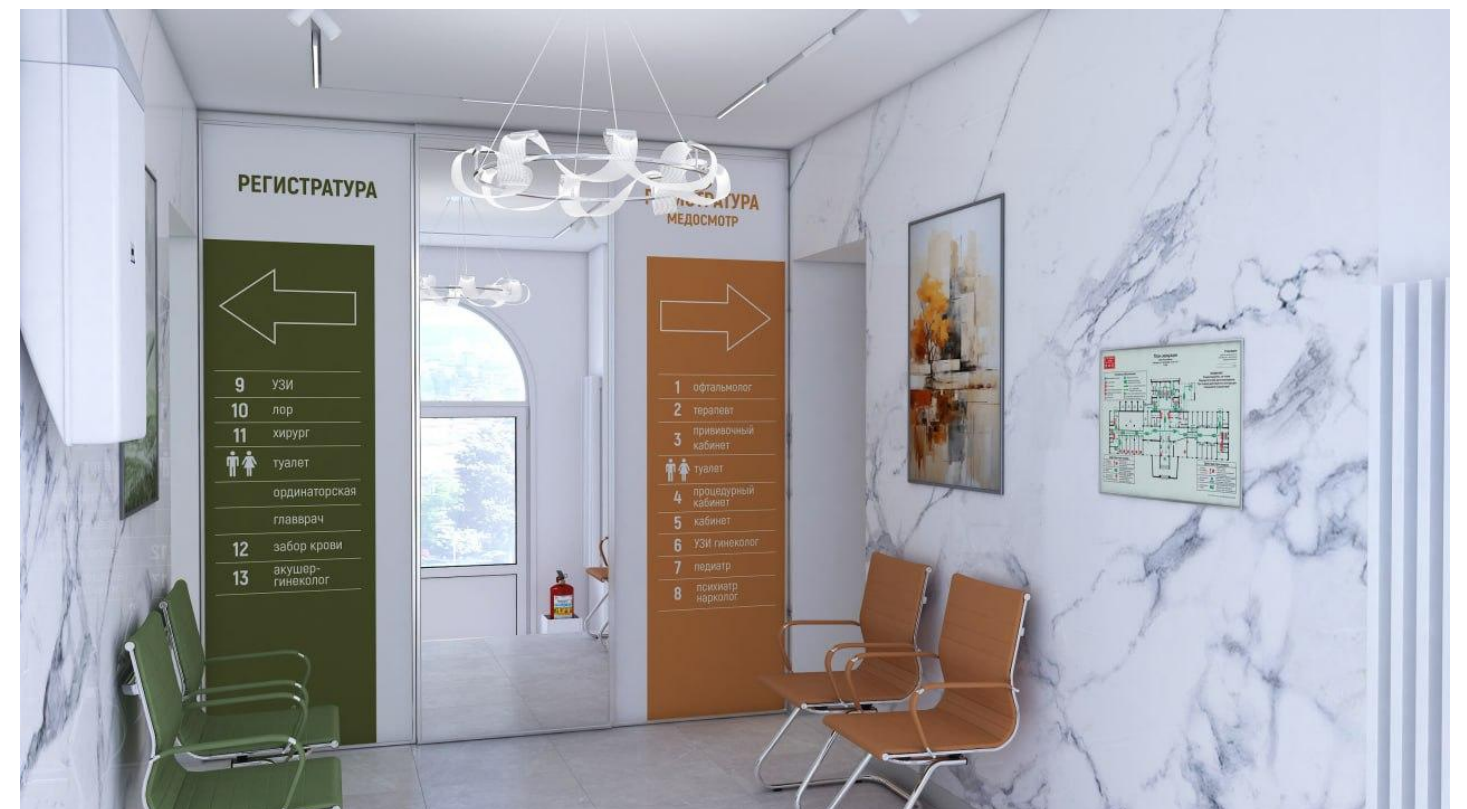

3Д картинки левого крыла медицинского центра

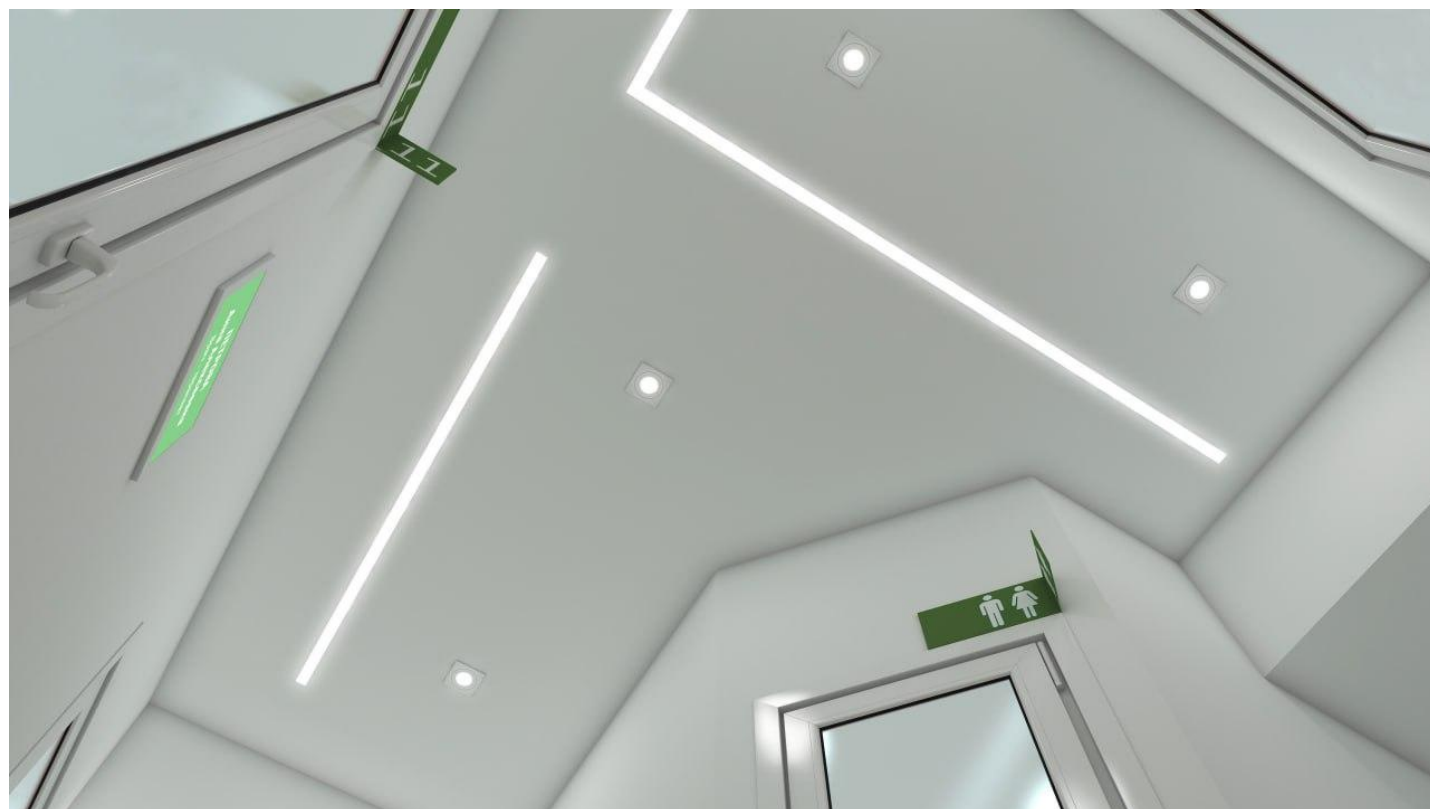

3Д картинки левого крыла медицинского центра

